

DETALHAMENTO TÉCNICO



NESTLÉ

PLANTA BAIXA




PLANTA
ESC.: 1:25

NESTLÉ


PLANTA BAIXA COM MALHA

Todos os direitos reservados. Proibida a reprodução total ou parcial sem autorização prévia por escrito.

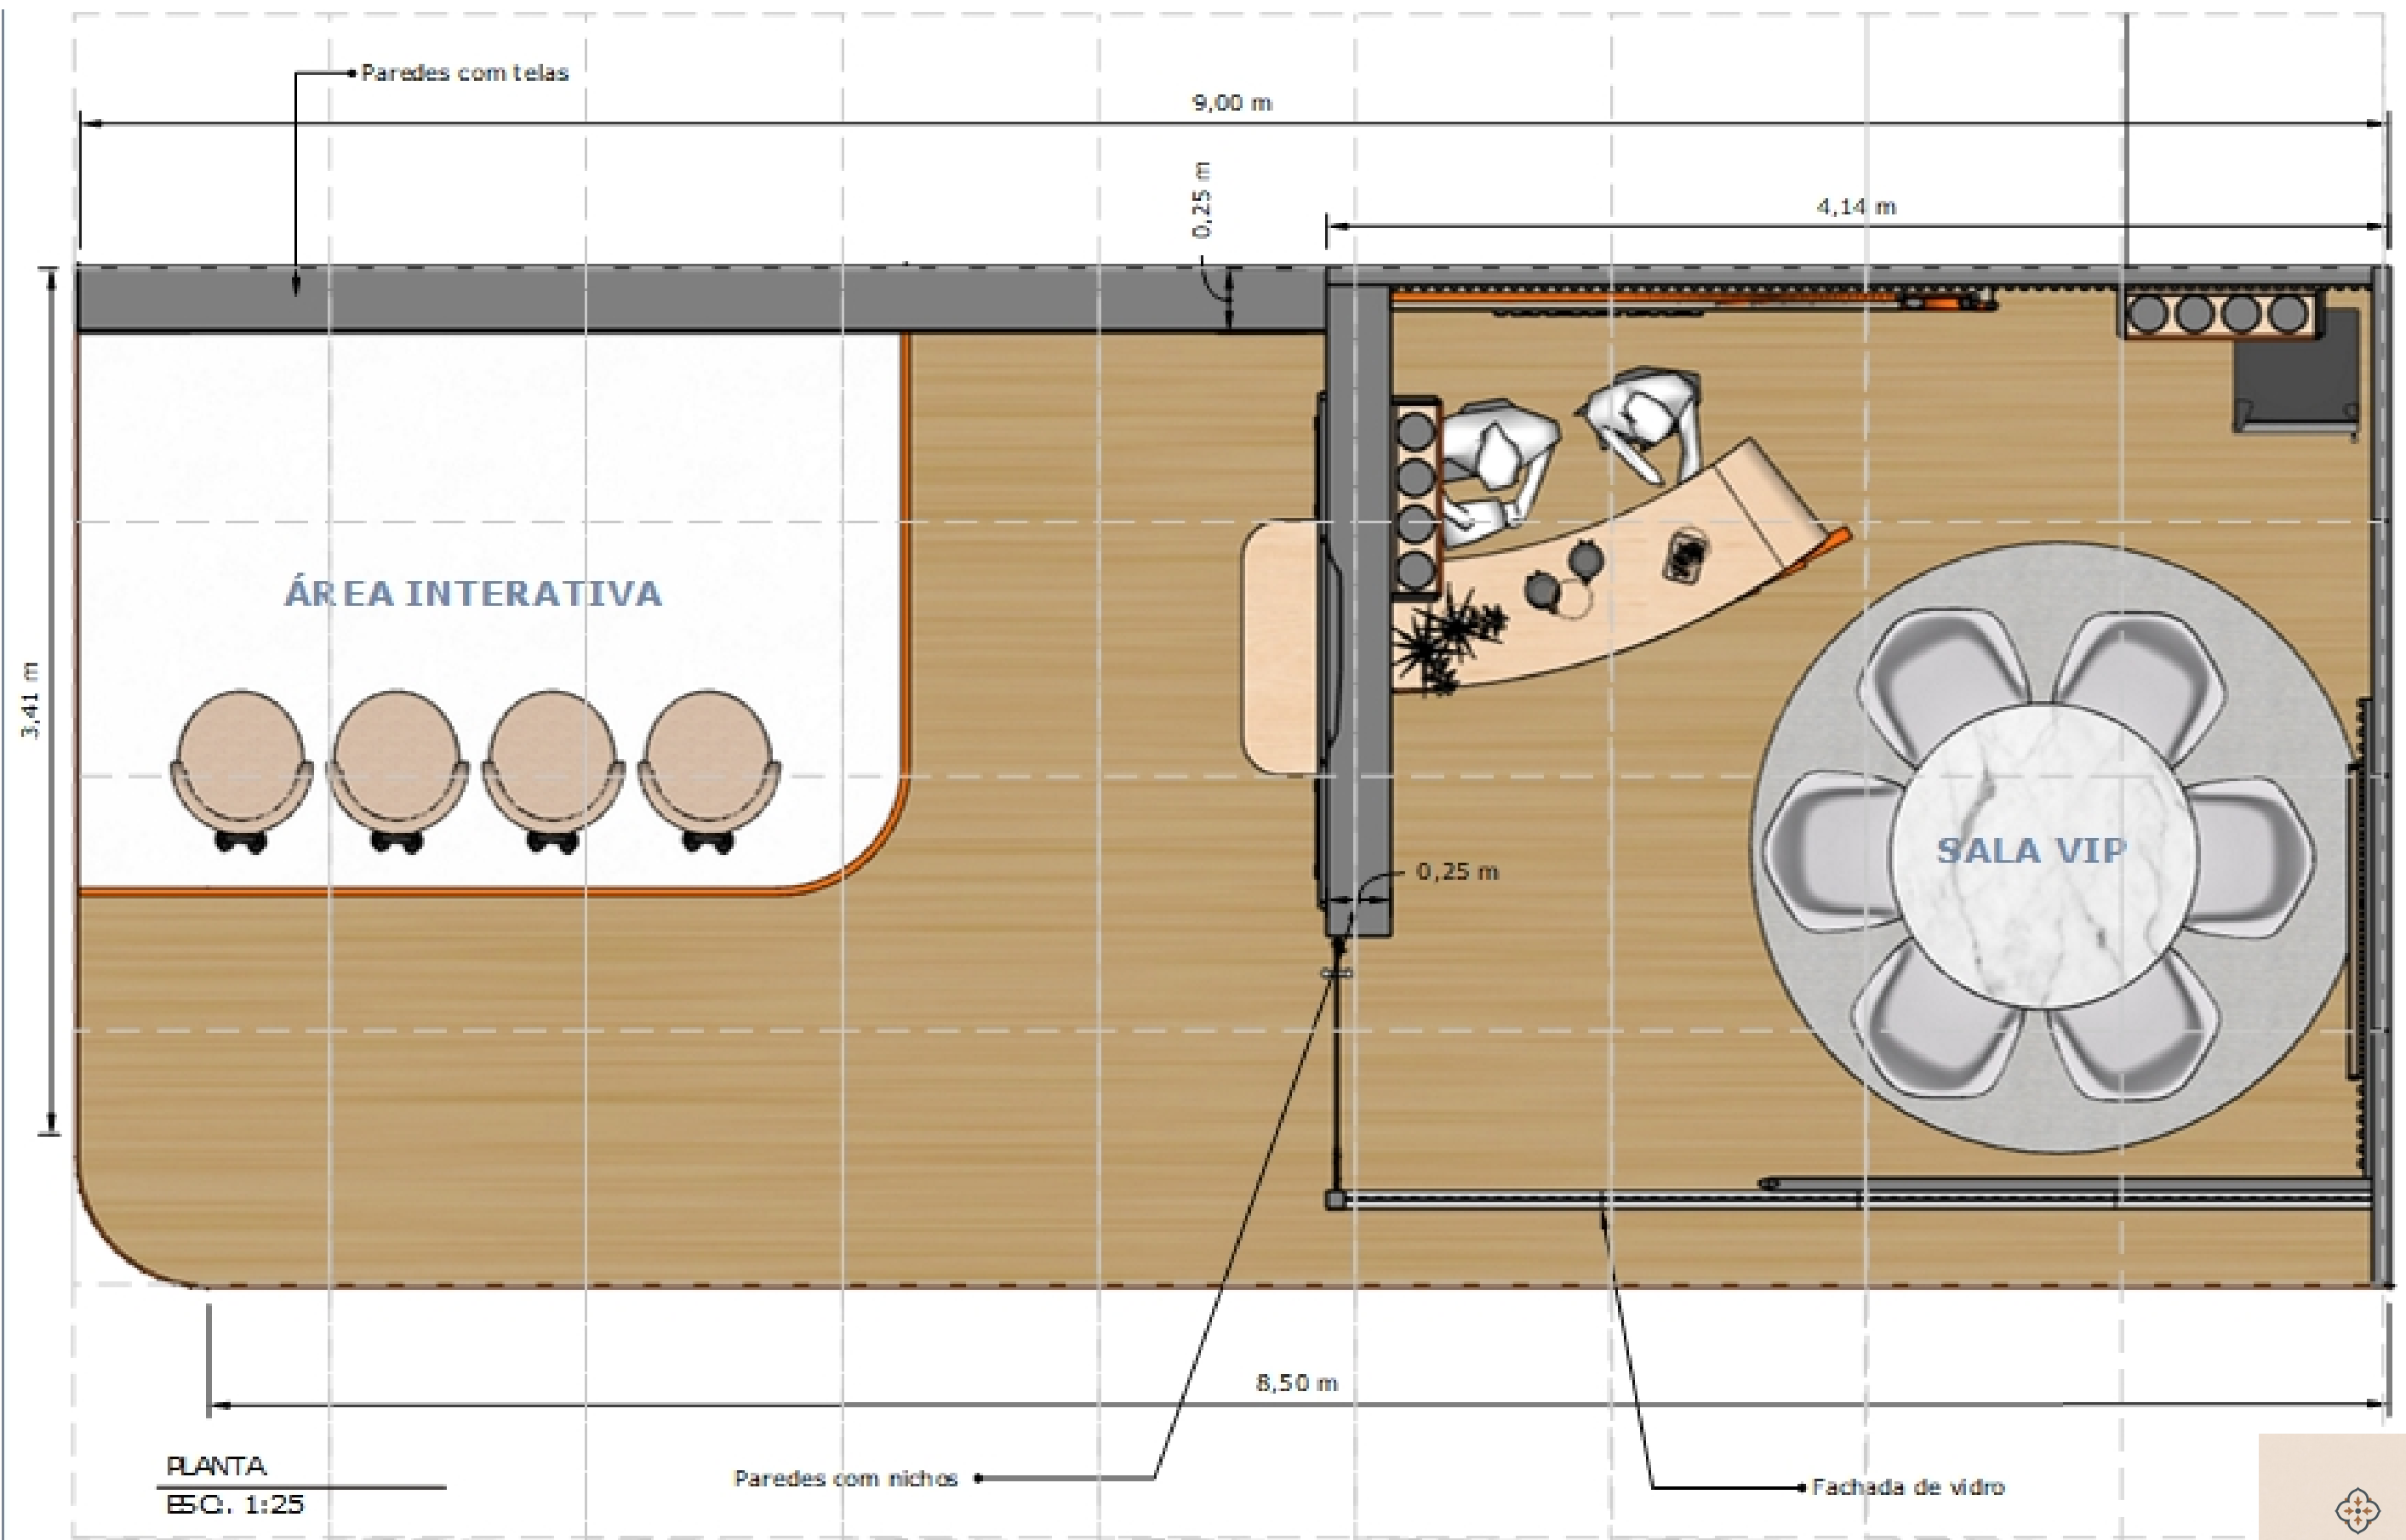


Malha de 1x1m

ESTRUTURA DE MONTAGEM

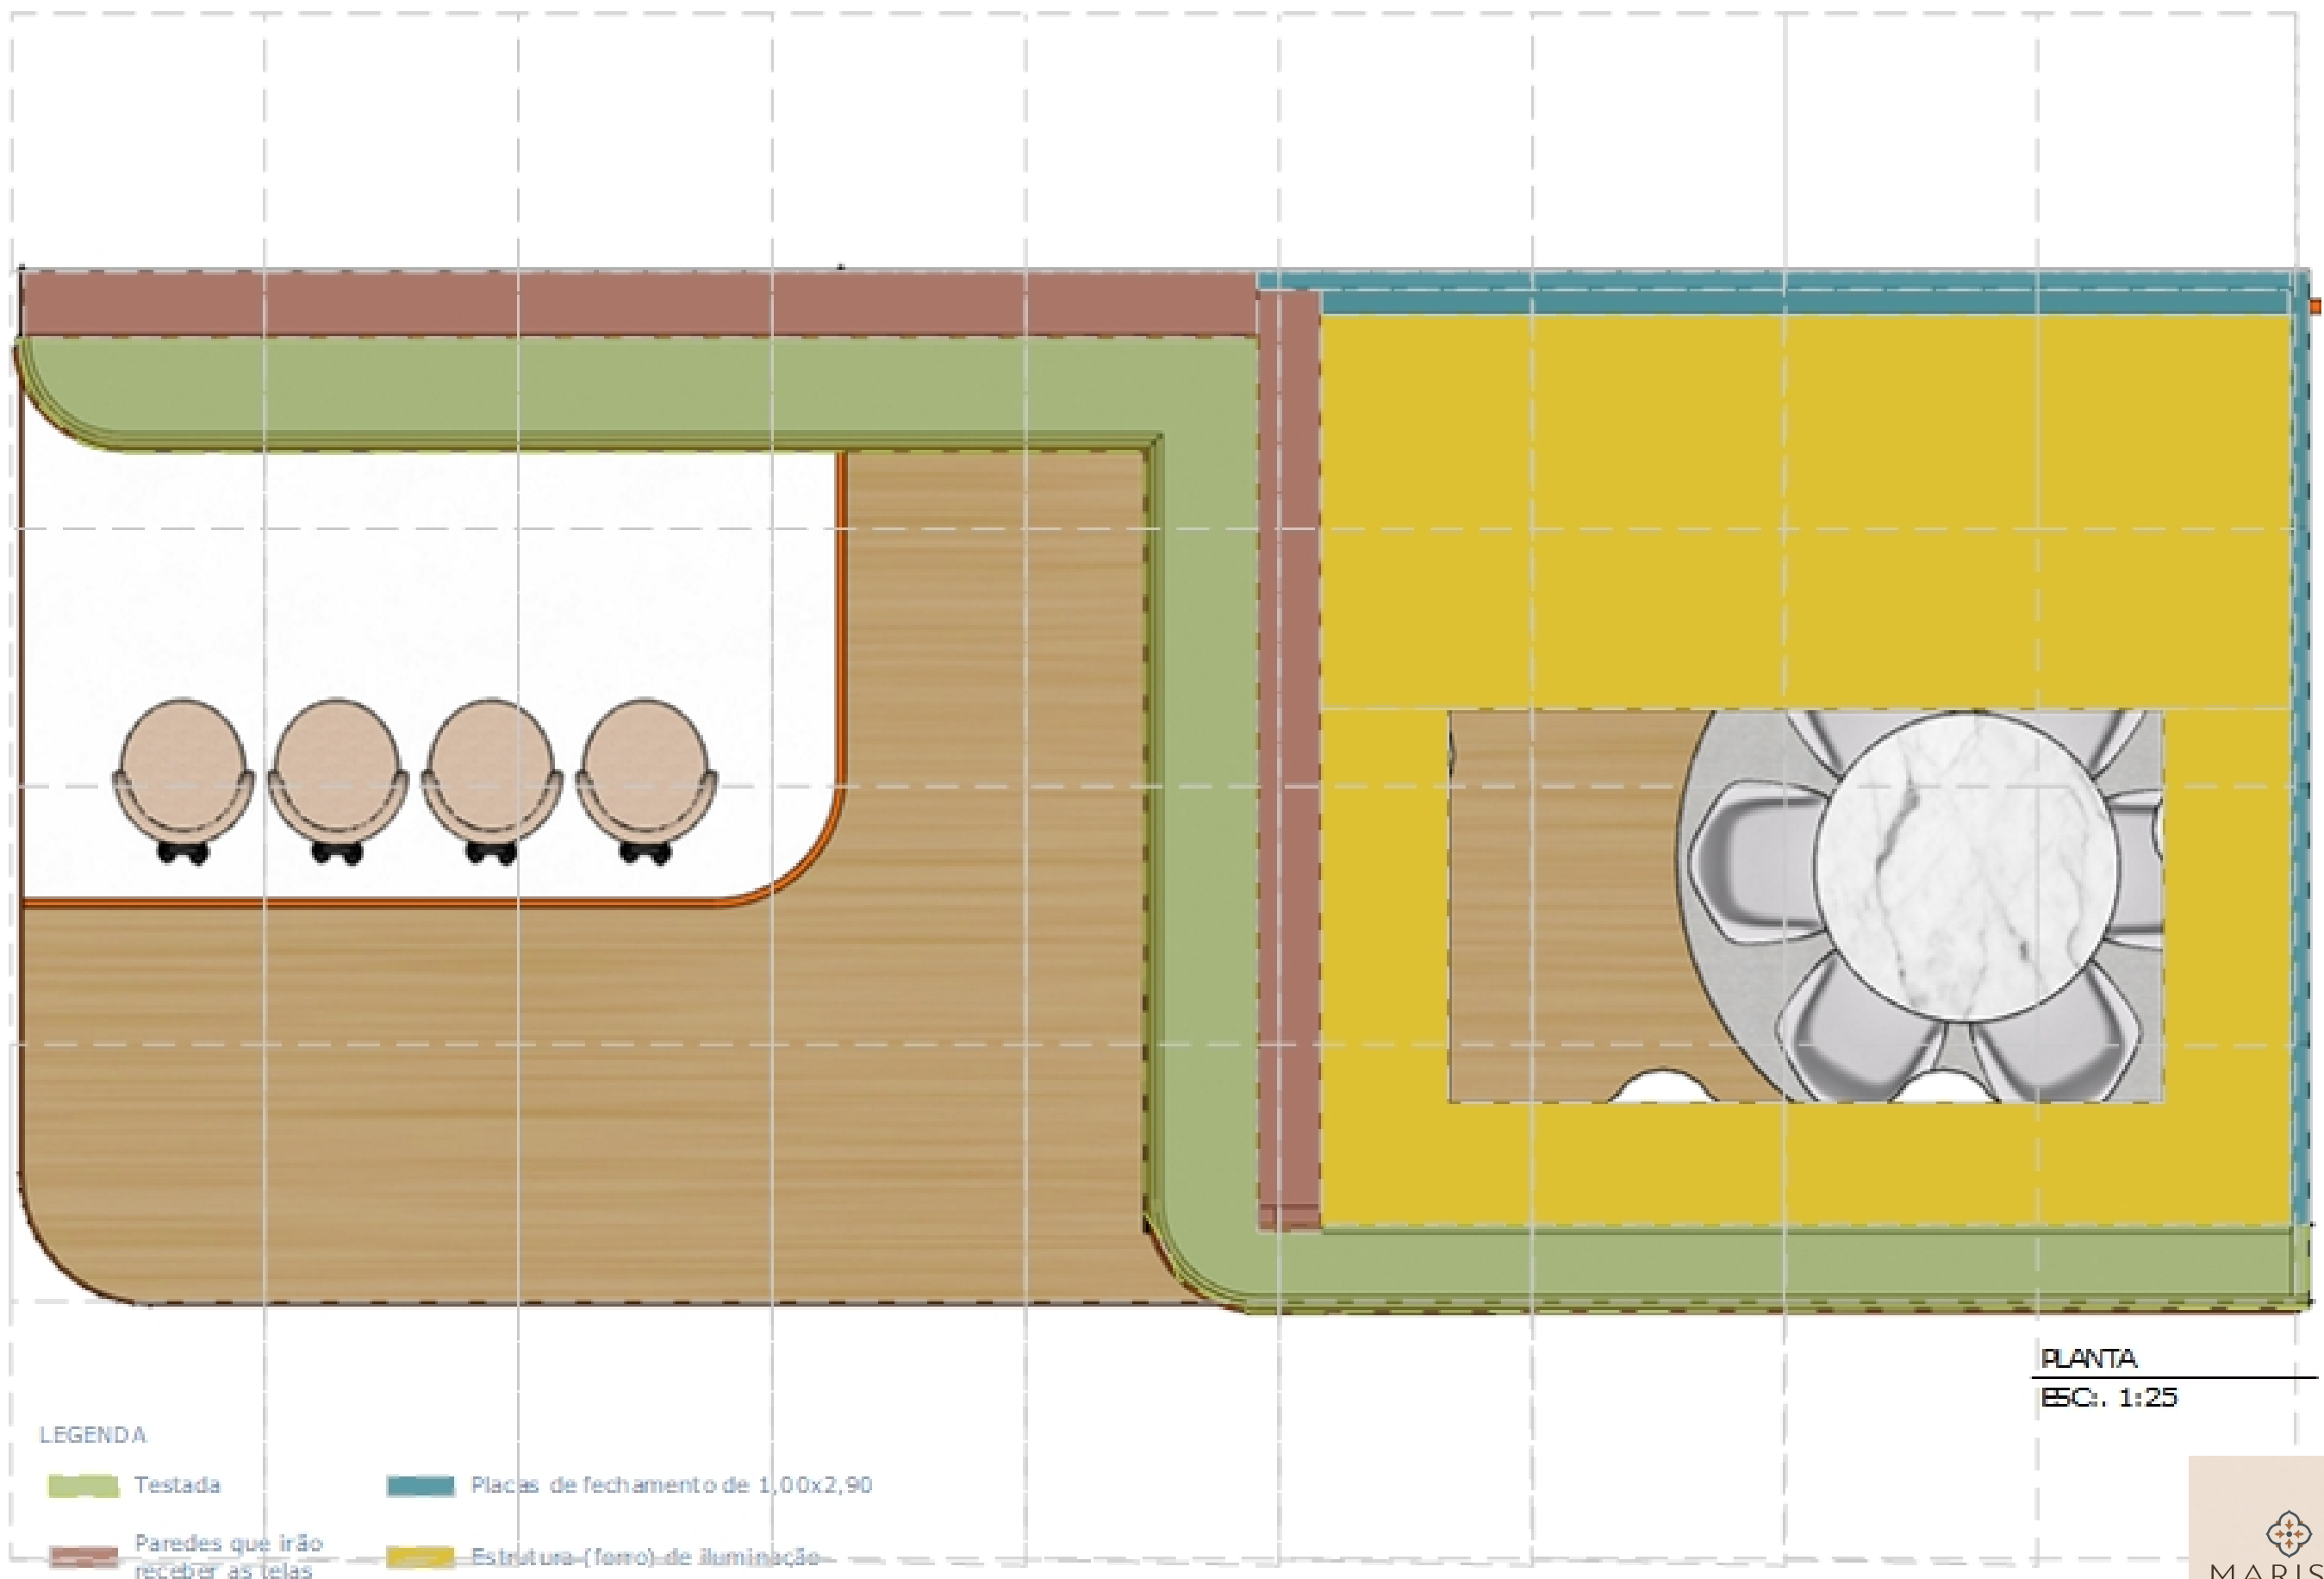


PERSPECTIVA ISOMÉTRICA

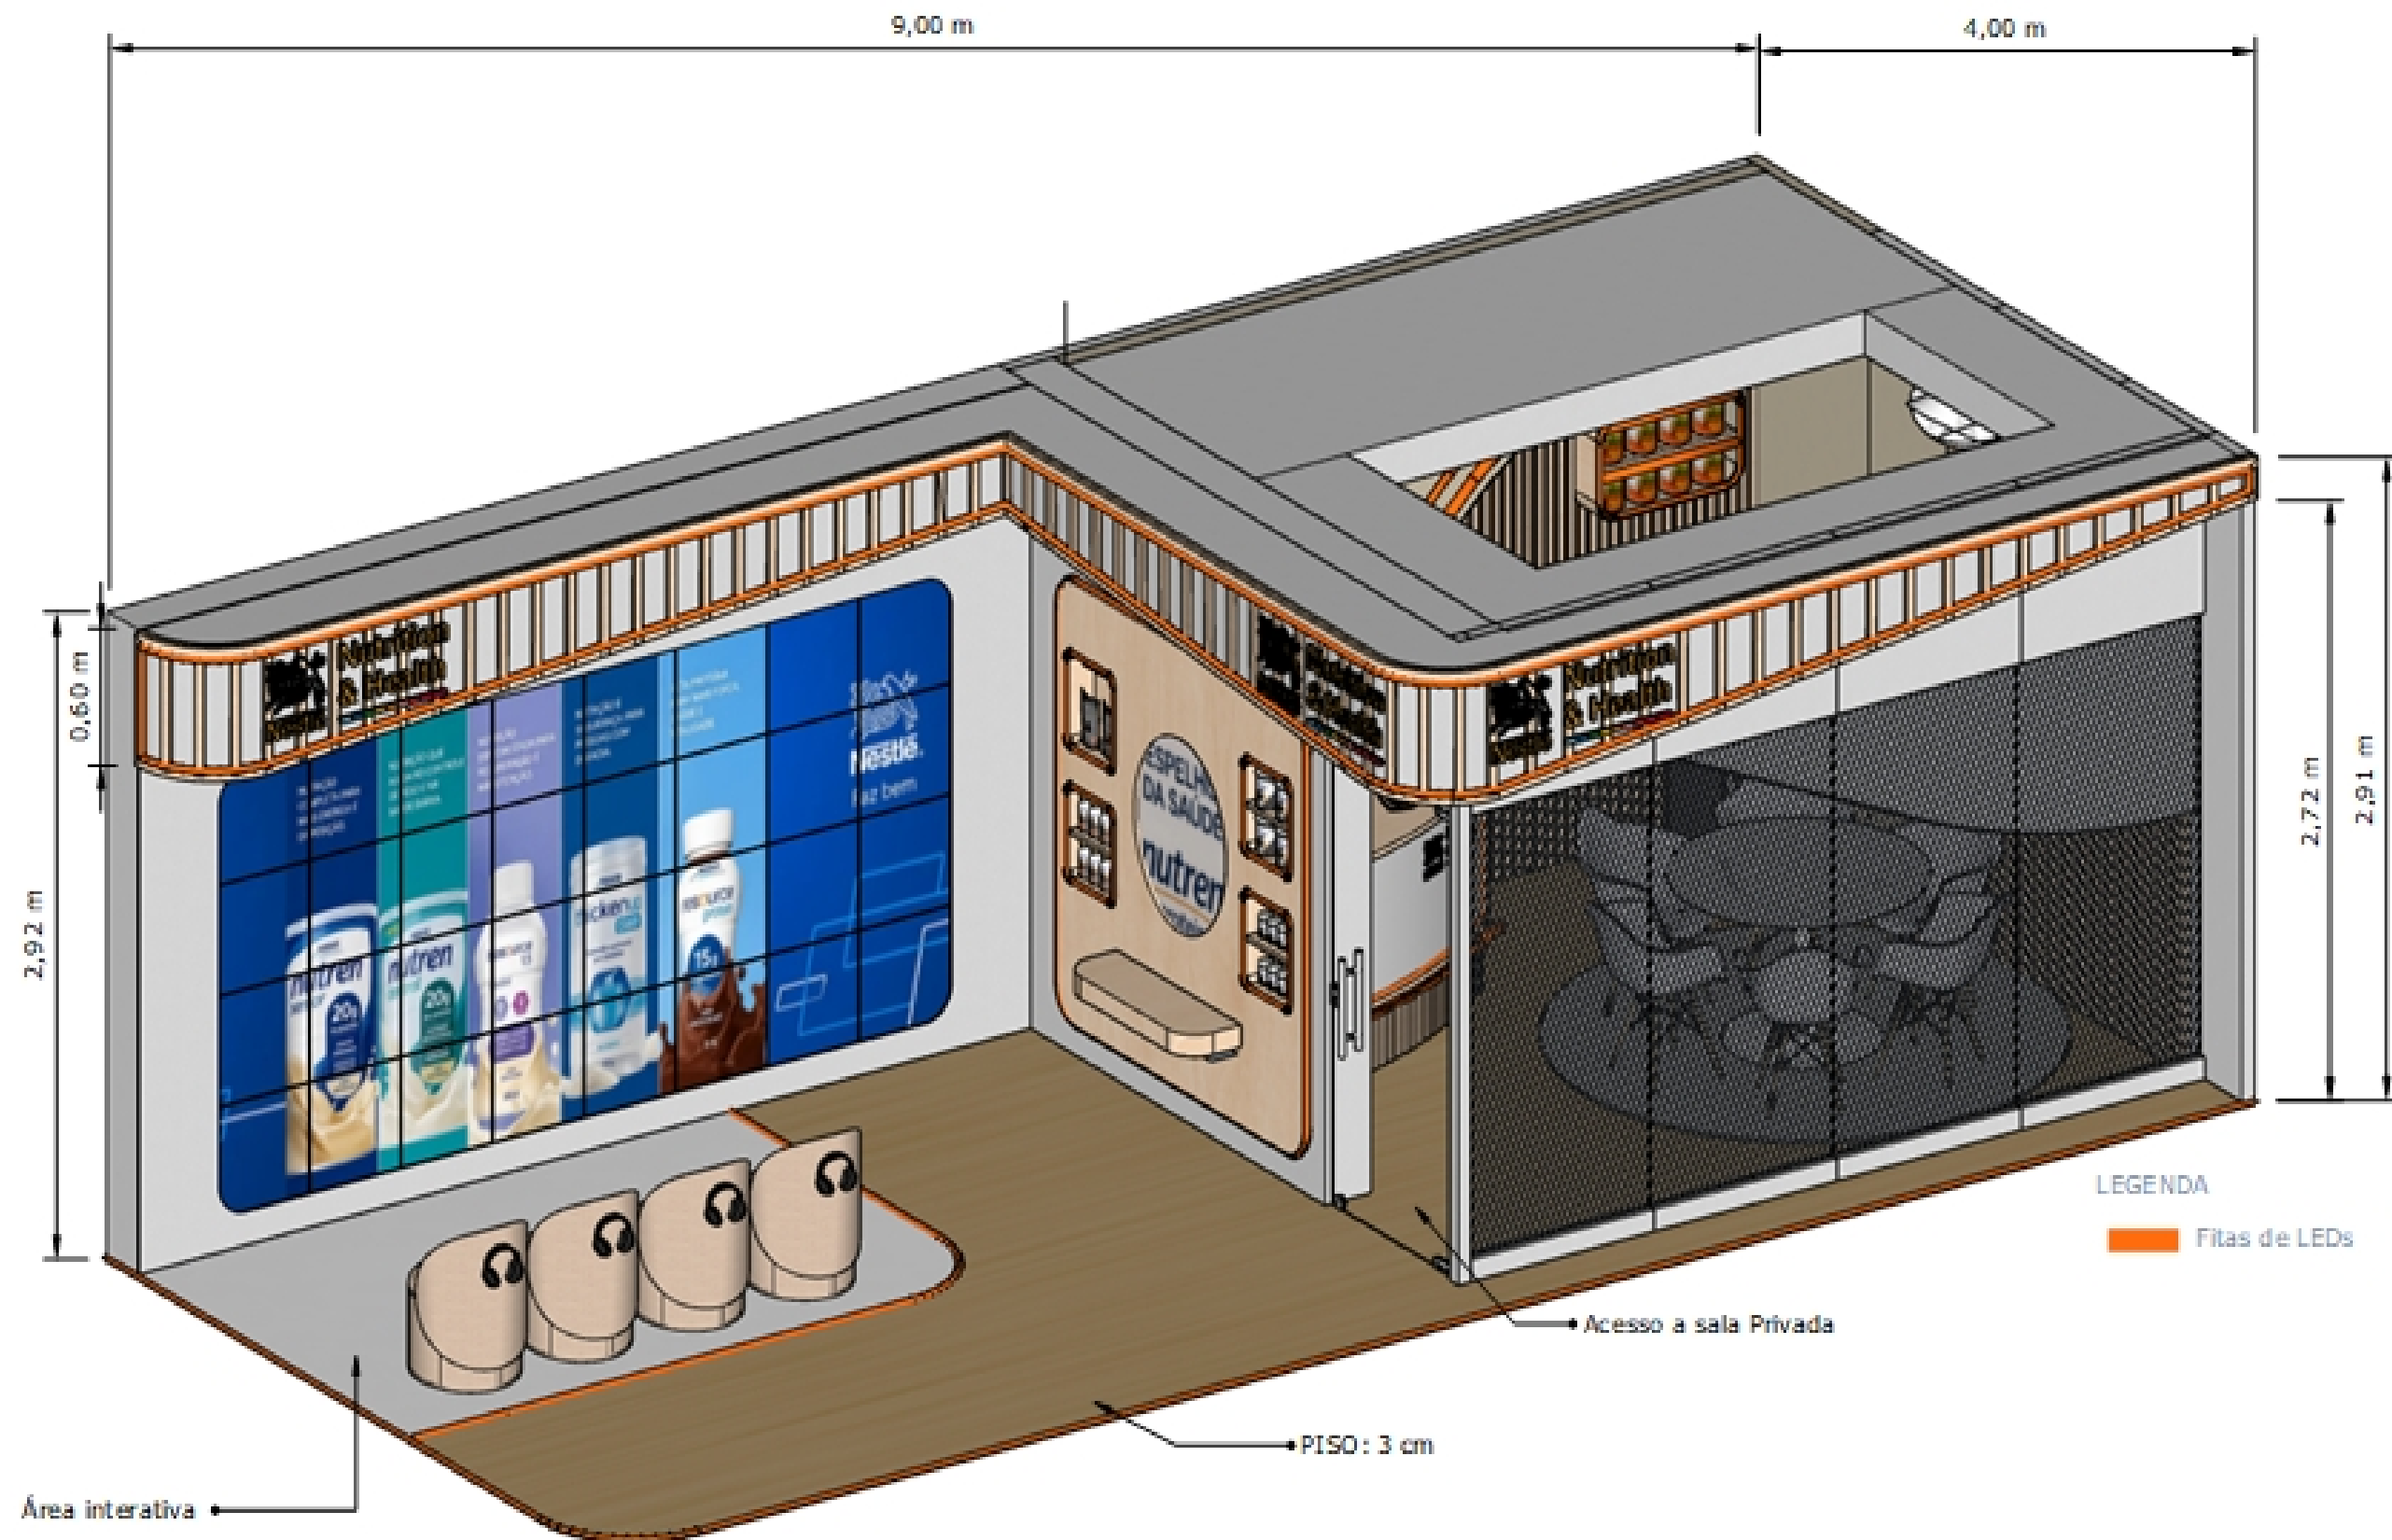

PERSPECTIVA
ESC. 1:25

Malha de 1x1m

LEDS

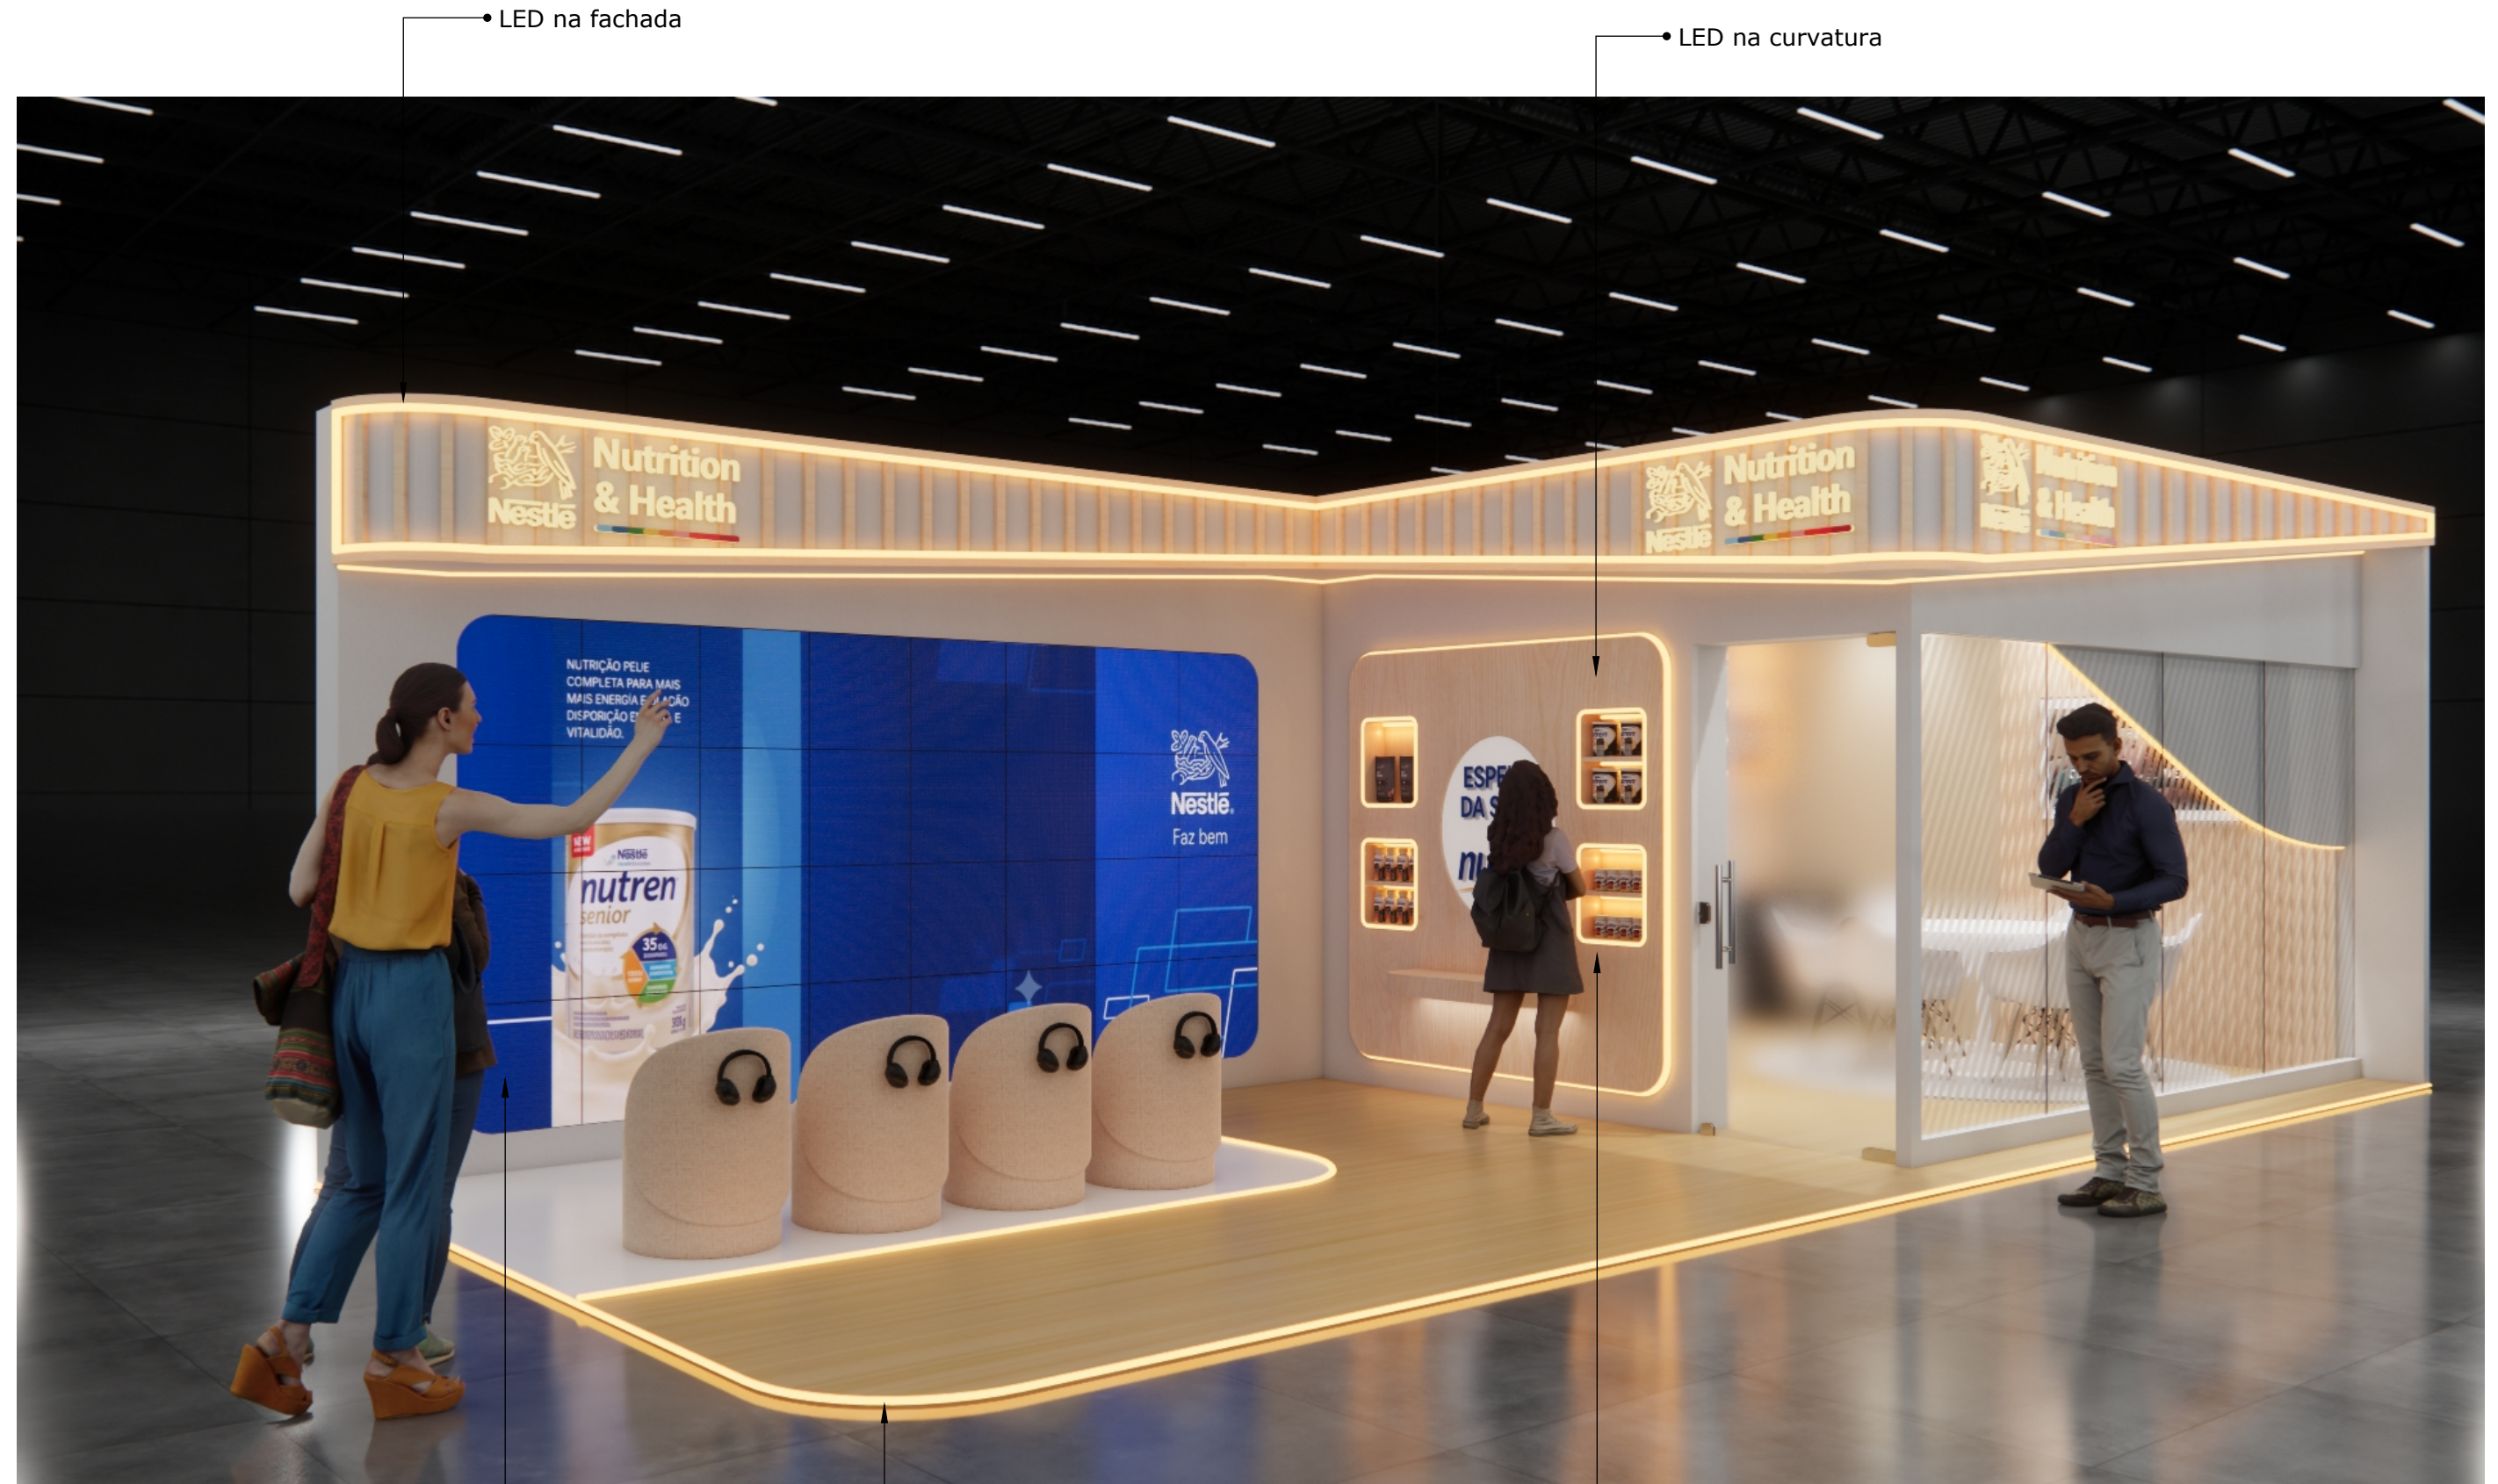

• LED na fachada


• LED na curvatura

TELAS •

• LED no piso

• LED em nichos

PERSPECTIVA ISOMÉTRICA

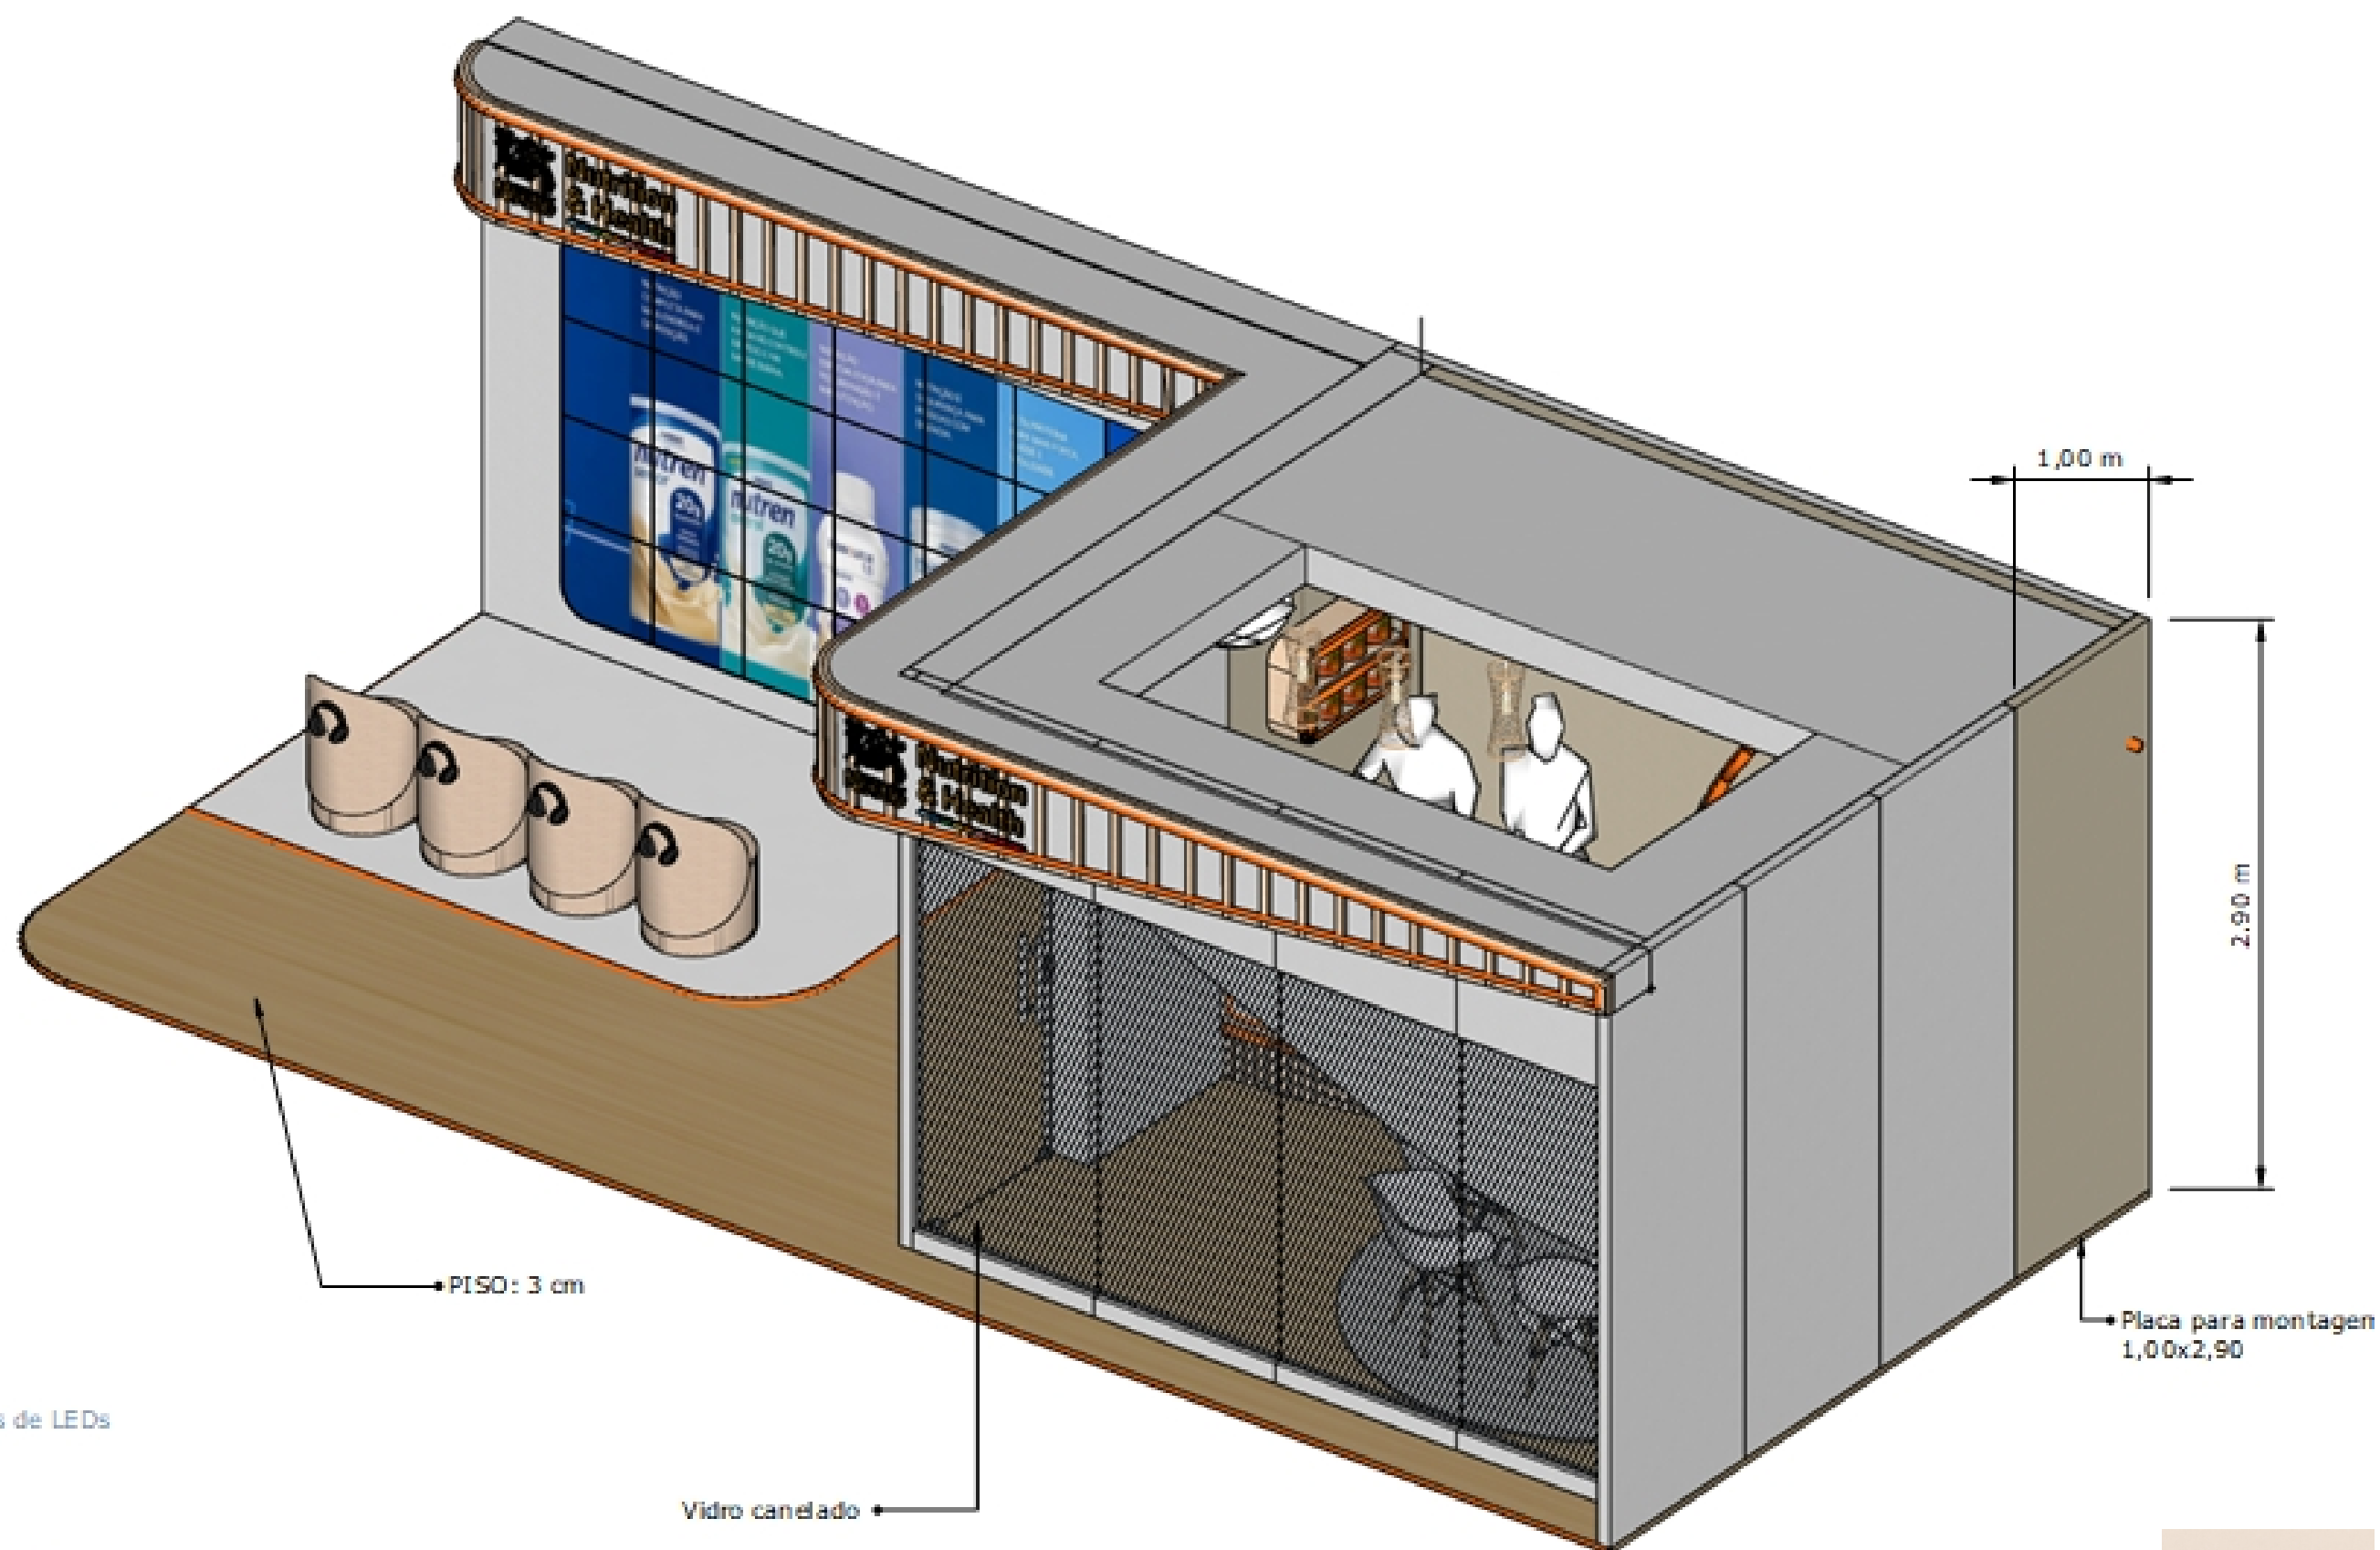

LEGENDA

 Fitas de LEDs

PERSPECTIVA
ESC. 1:25

Malha de 1x1m


LEDs



Vidro cancelado

Curvatura iluminada


FACHADA FRONTAL

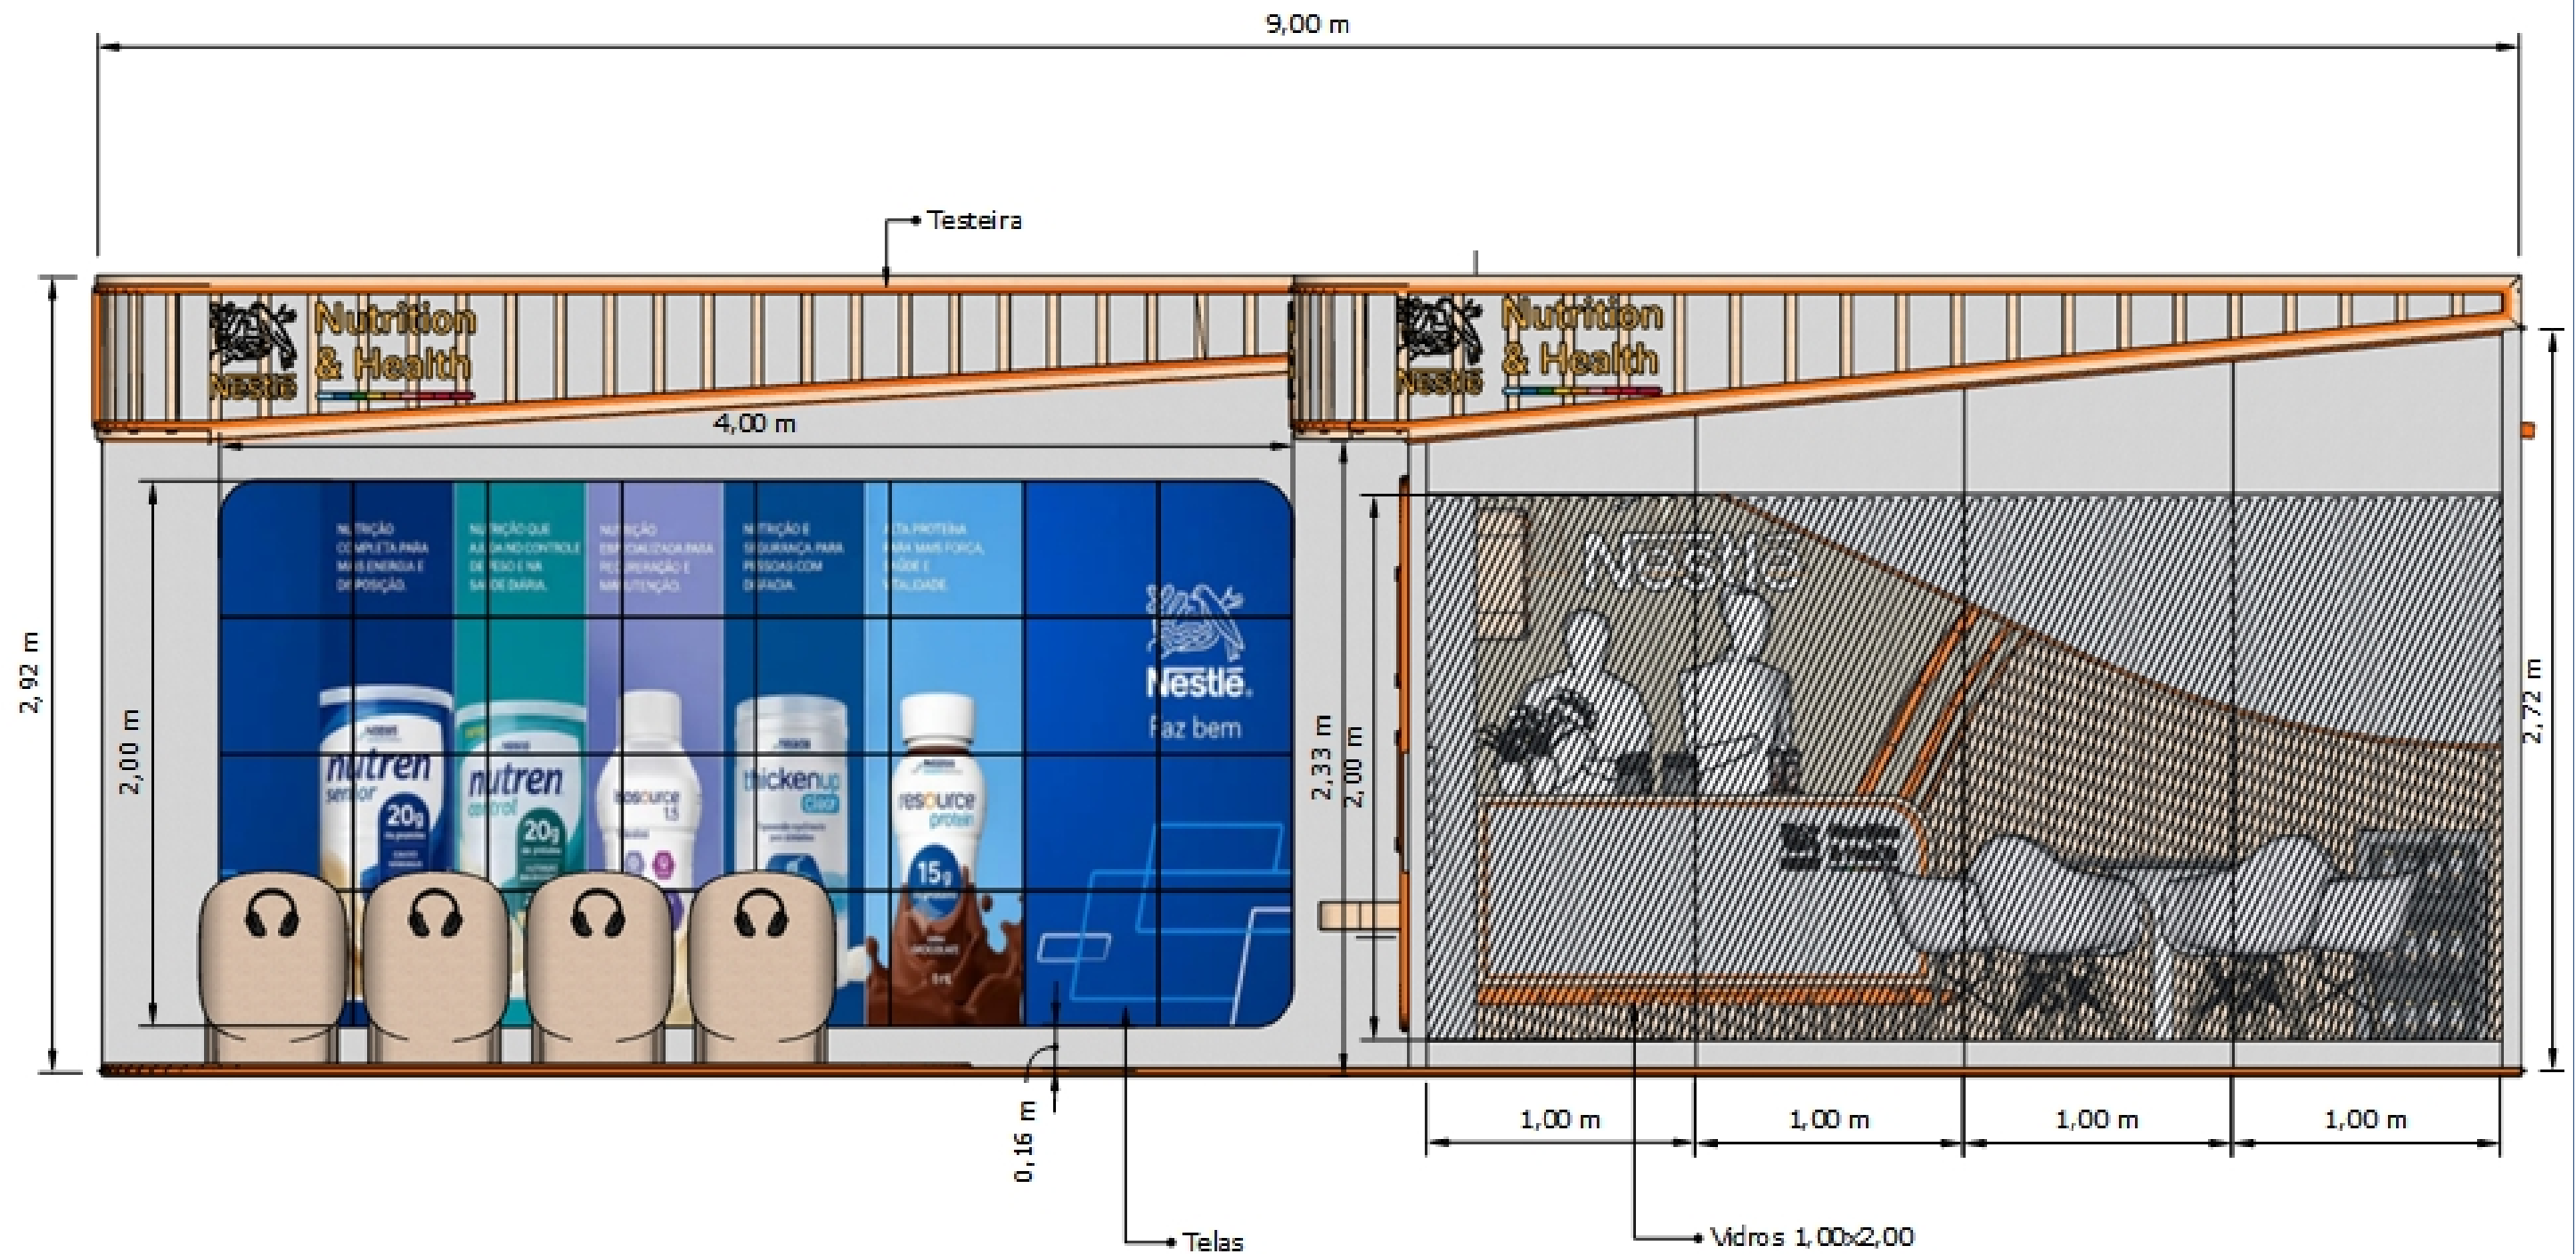

VISTA FRONTAL
ESQ. 1:25

Malha de 1x1m

FACHADA ESQUERDA

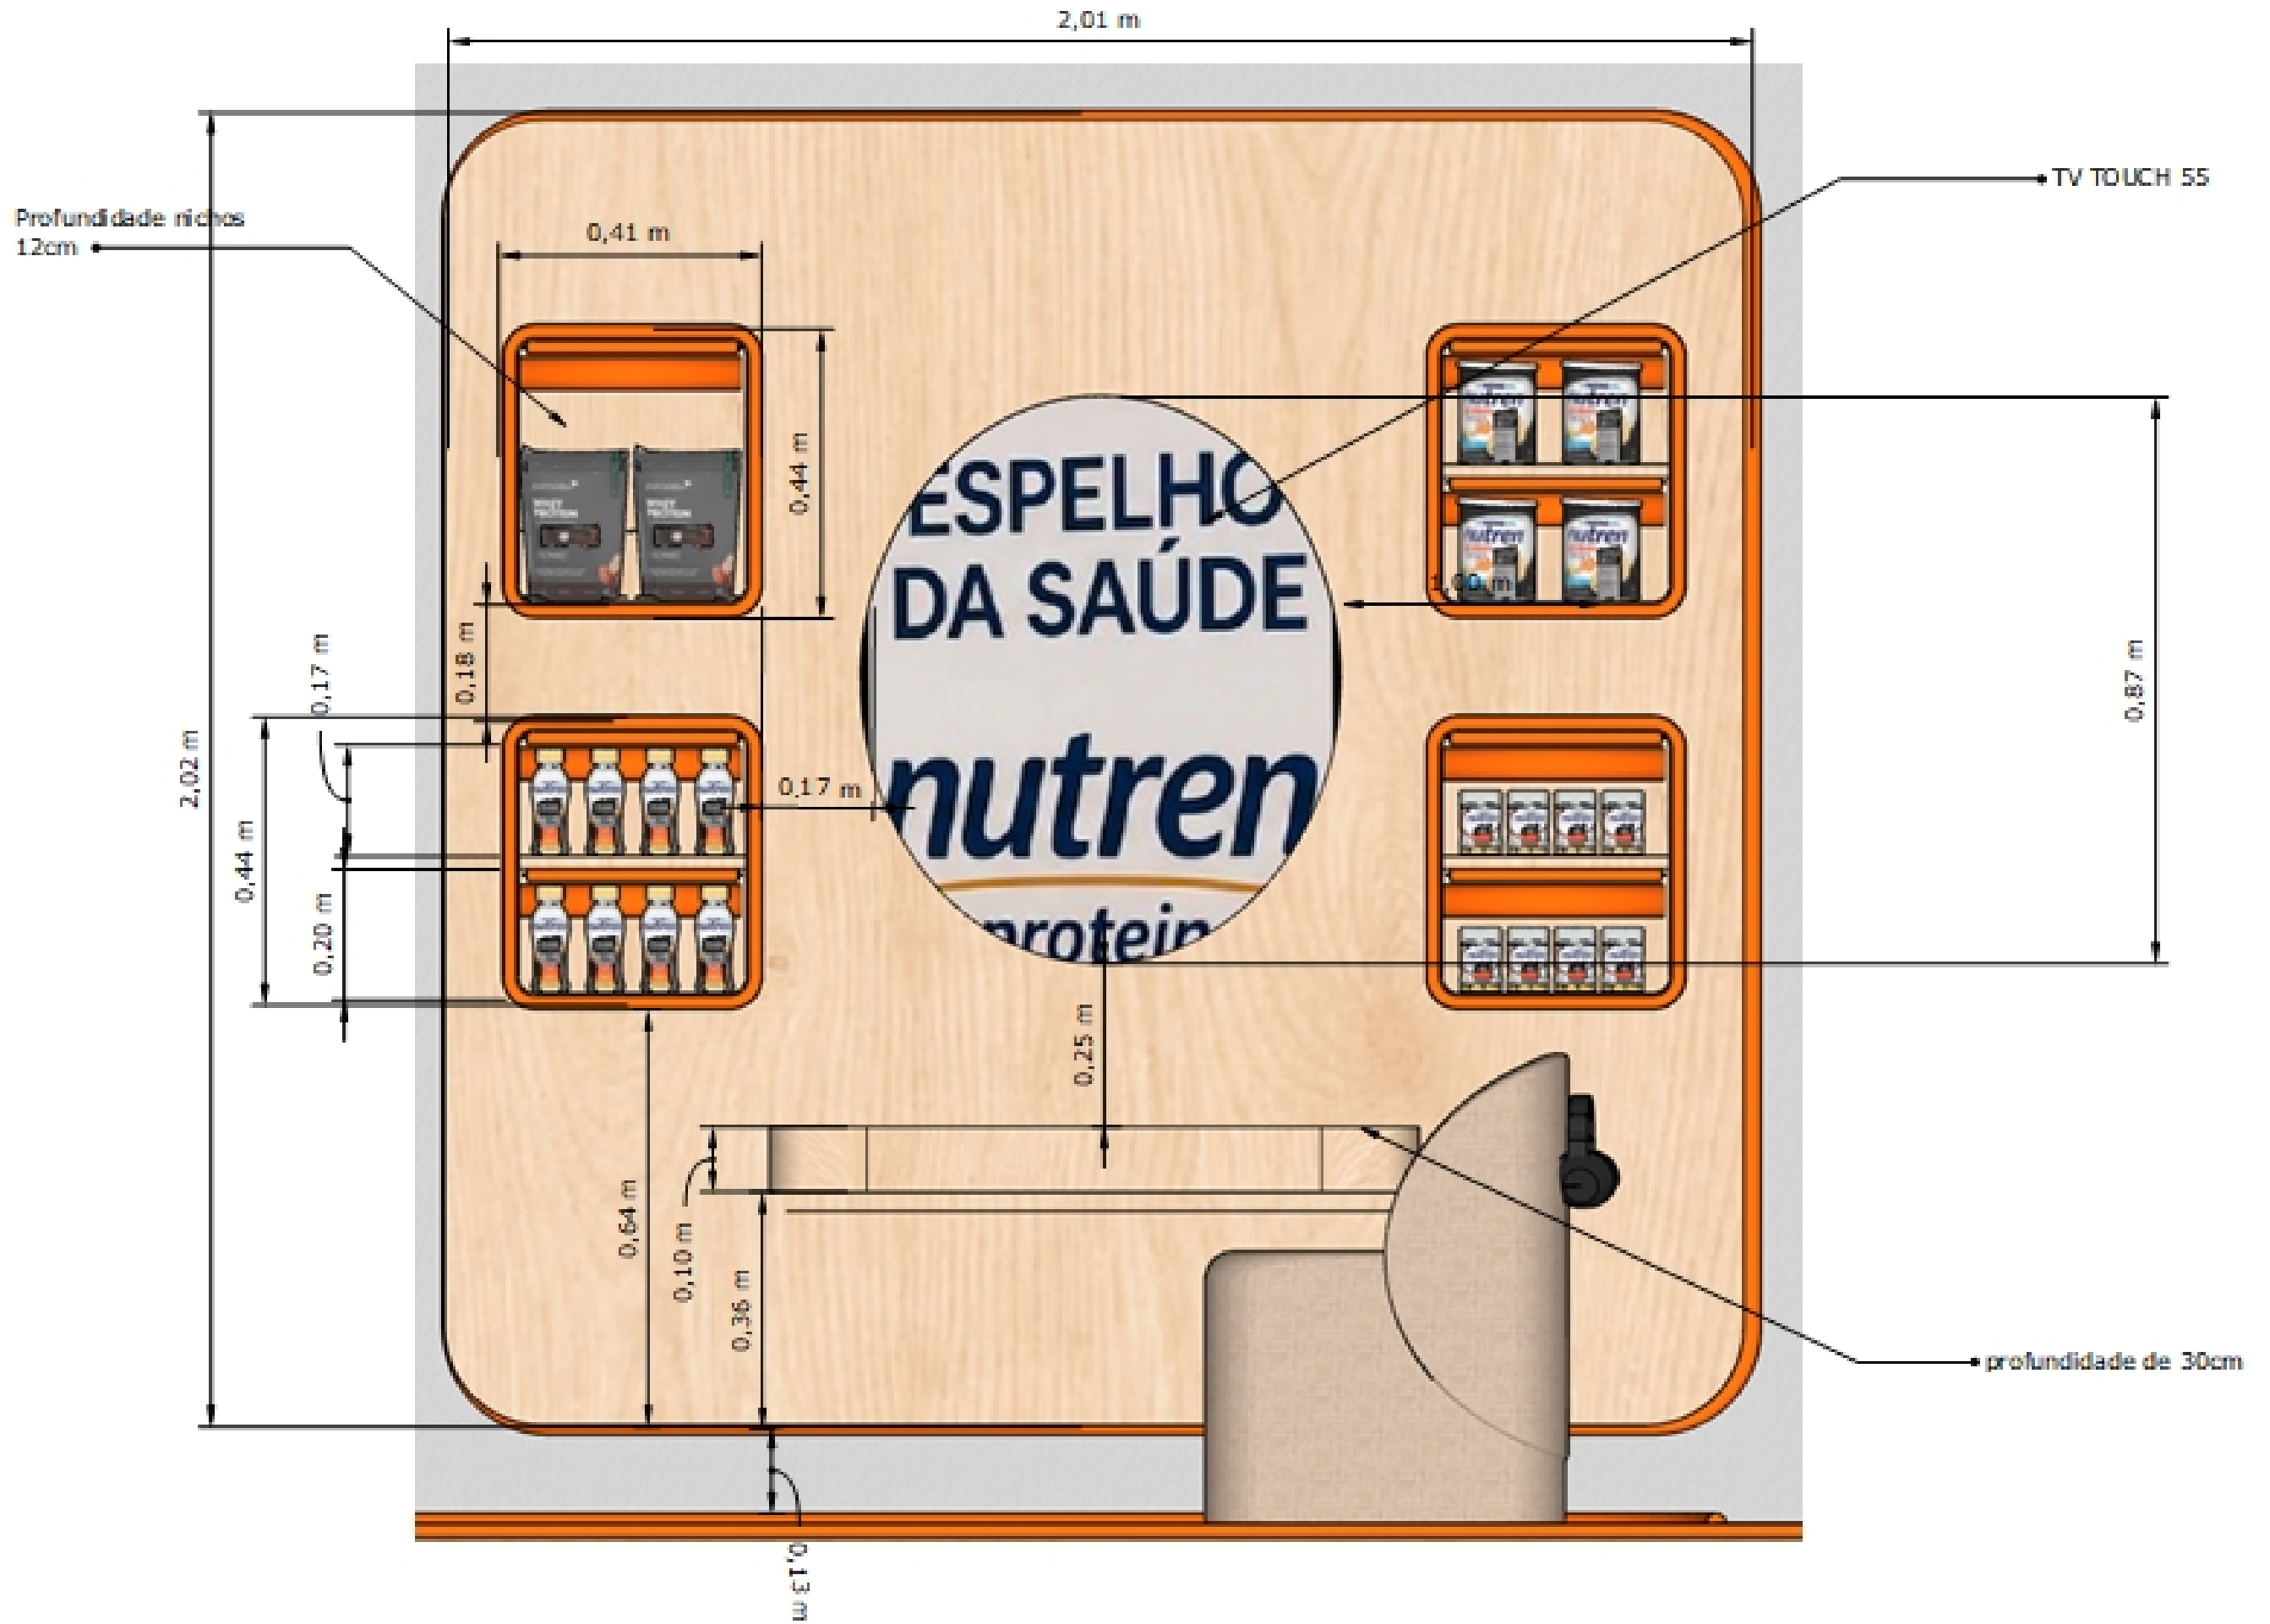


2,01 m



FACHADA ESQUERDA



TESTADA

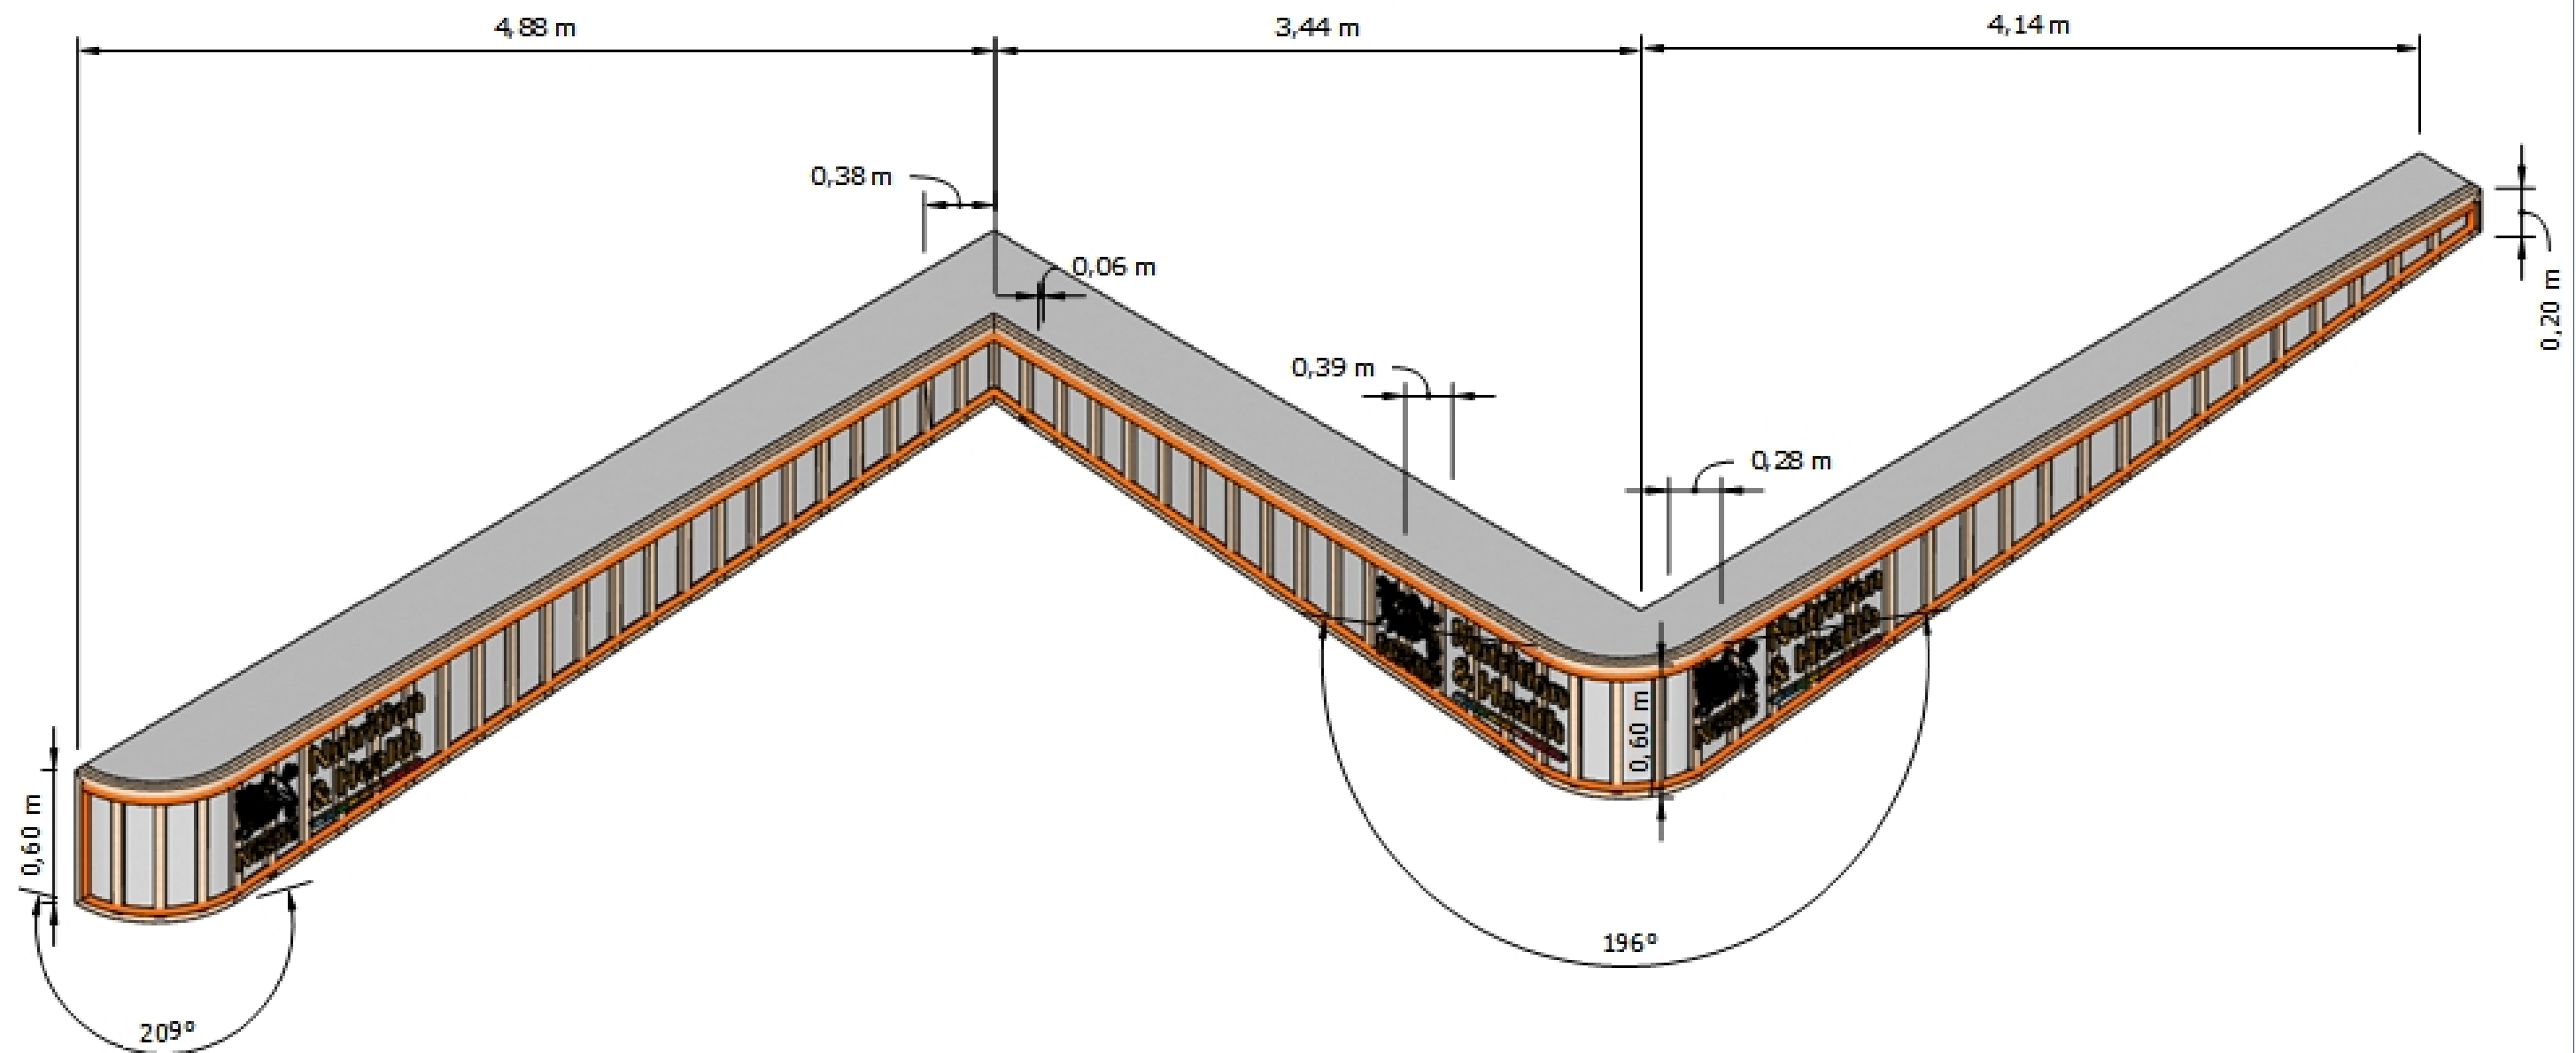

LEGENDA


 Fitas de LEDs

PERSPECTIVA

ESQ. 1:25

Malha de 1x1m

TESTADA

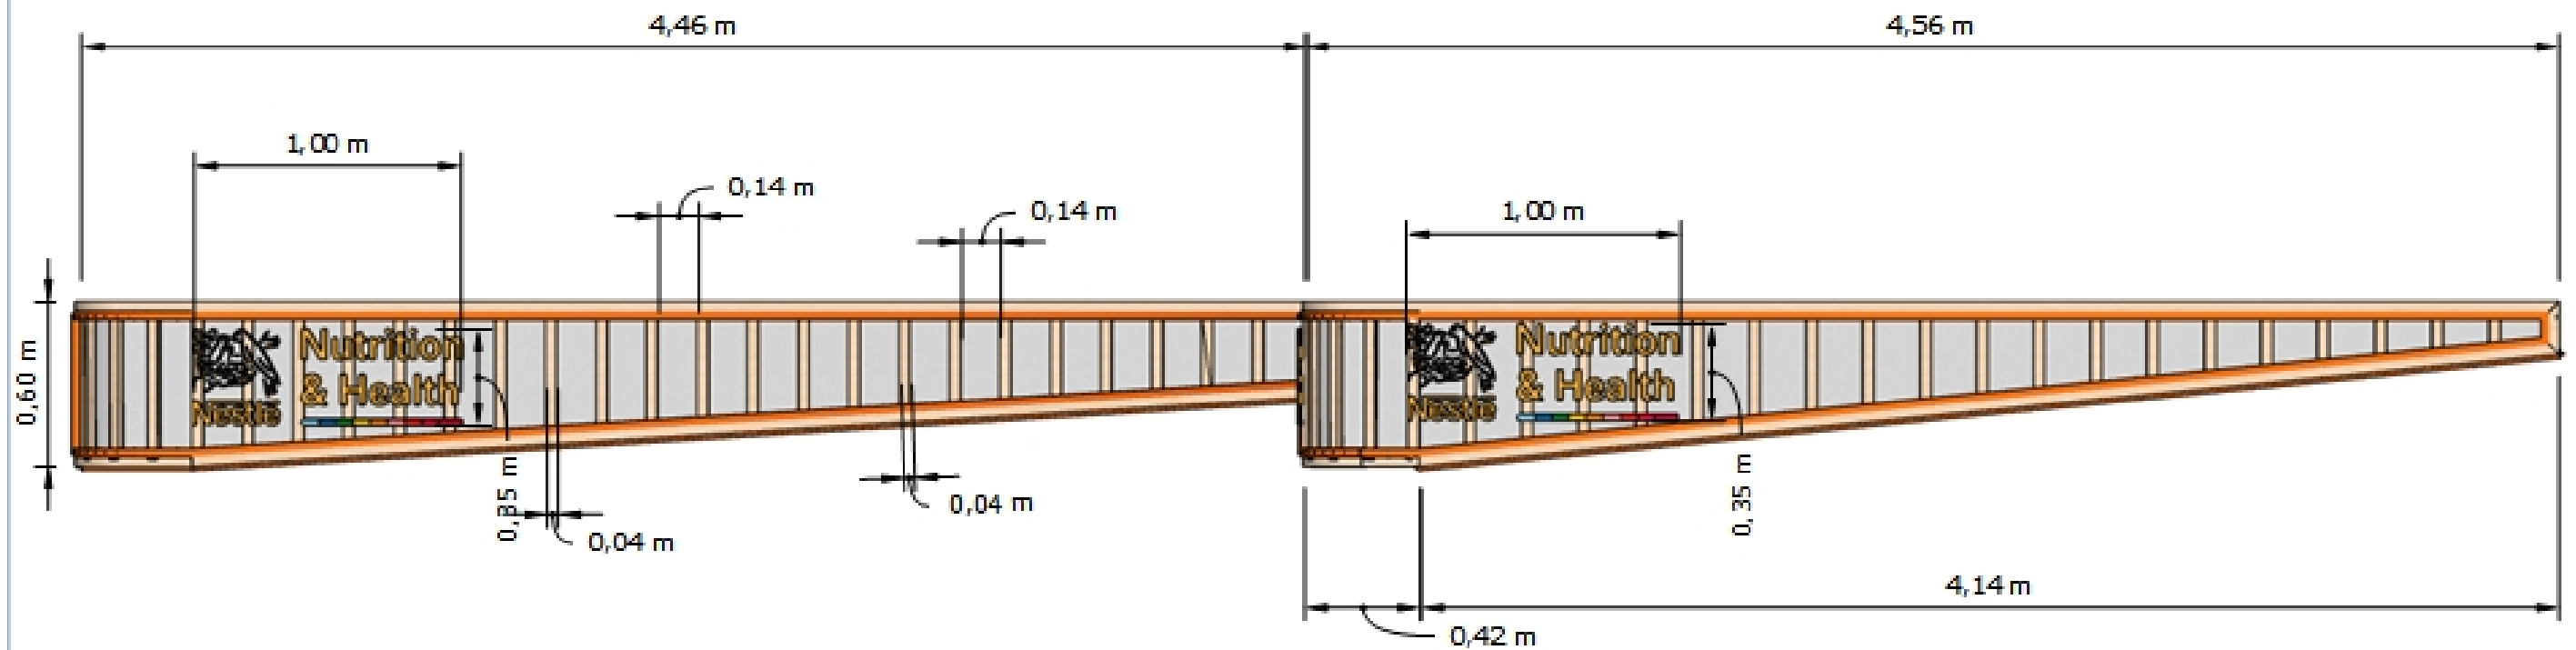


VISTA FRONTAL

ESQ. 1:25

LEGENDA

 Fitas de LEDs

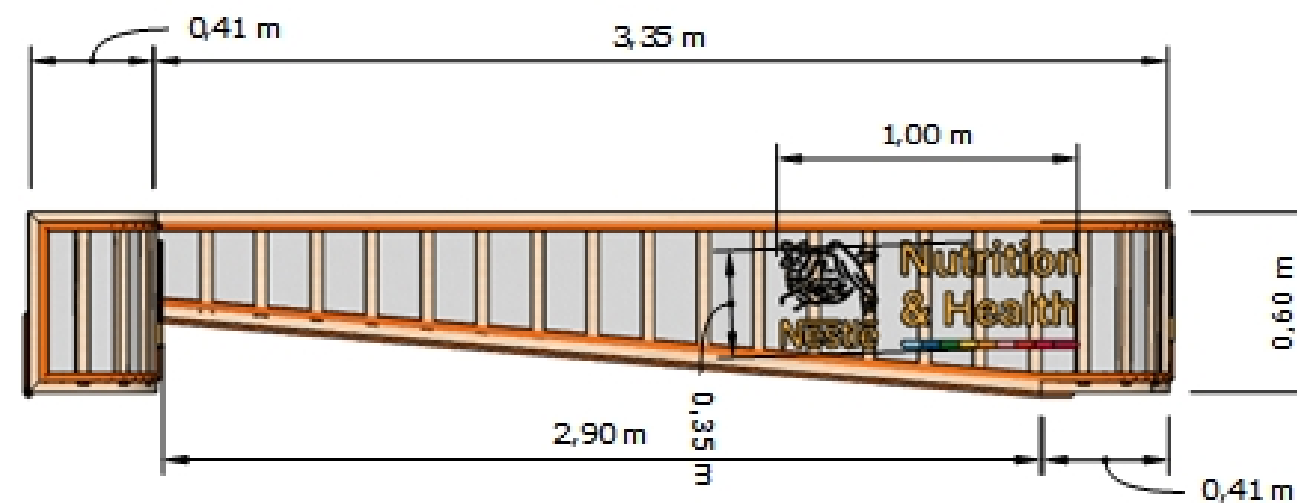

VISTA ESQUERDA

ESQ. 1:25


Malha de 1x1m

TESTADA

Todos os direitos reservados. Proibida a reprodução total ou parcial sem autorização prévia por escrito.



PLANTA DE ILUMINAÇÃO

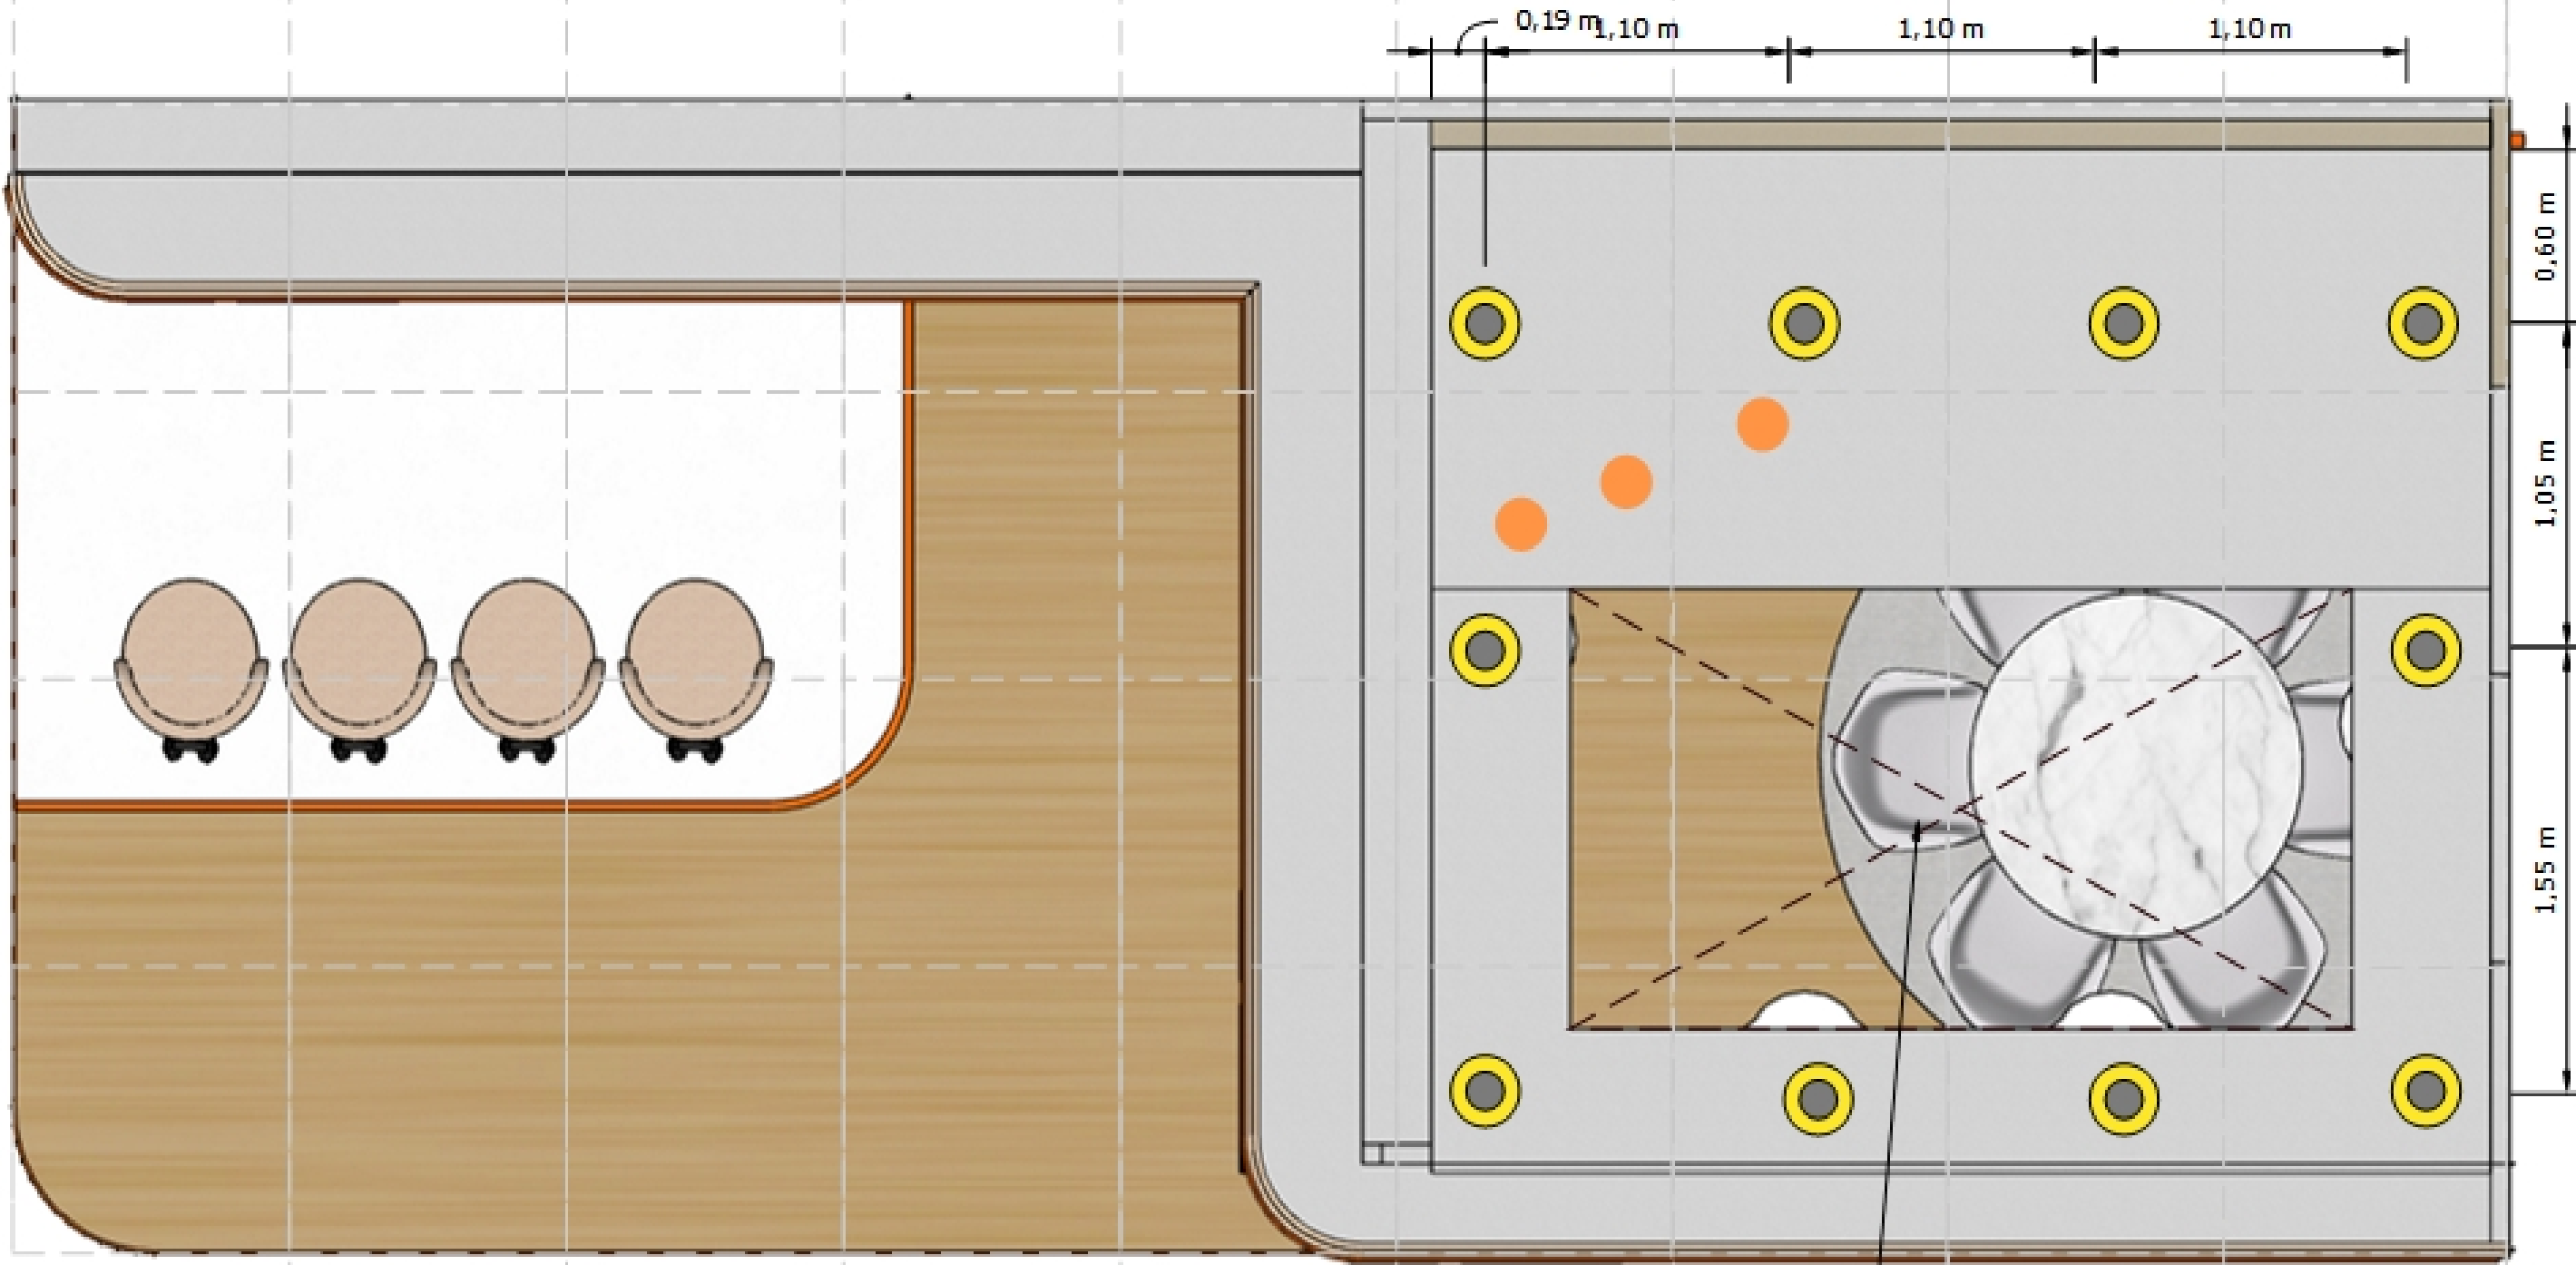

LEGENDA:



Ponto de tomada
Simples



Ponto de tomada
dupla



Ponto de energia



QE quadro de
energia



Ponto de luz



Ponto dos pendent

Vão forro

PLANTA

ESC.: 1:25


SALA VIP - IMAGEM



• Plfons de embutir


PLANTA ELÉTRICA

Todos os direitos reservados. Proibida a reprodução total ou parcial sem autorização prévia por escrito.

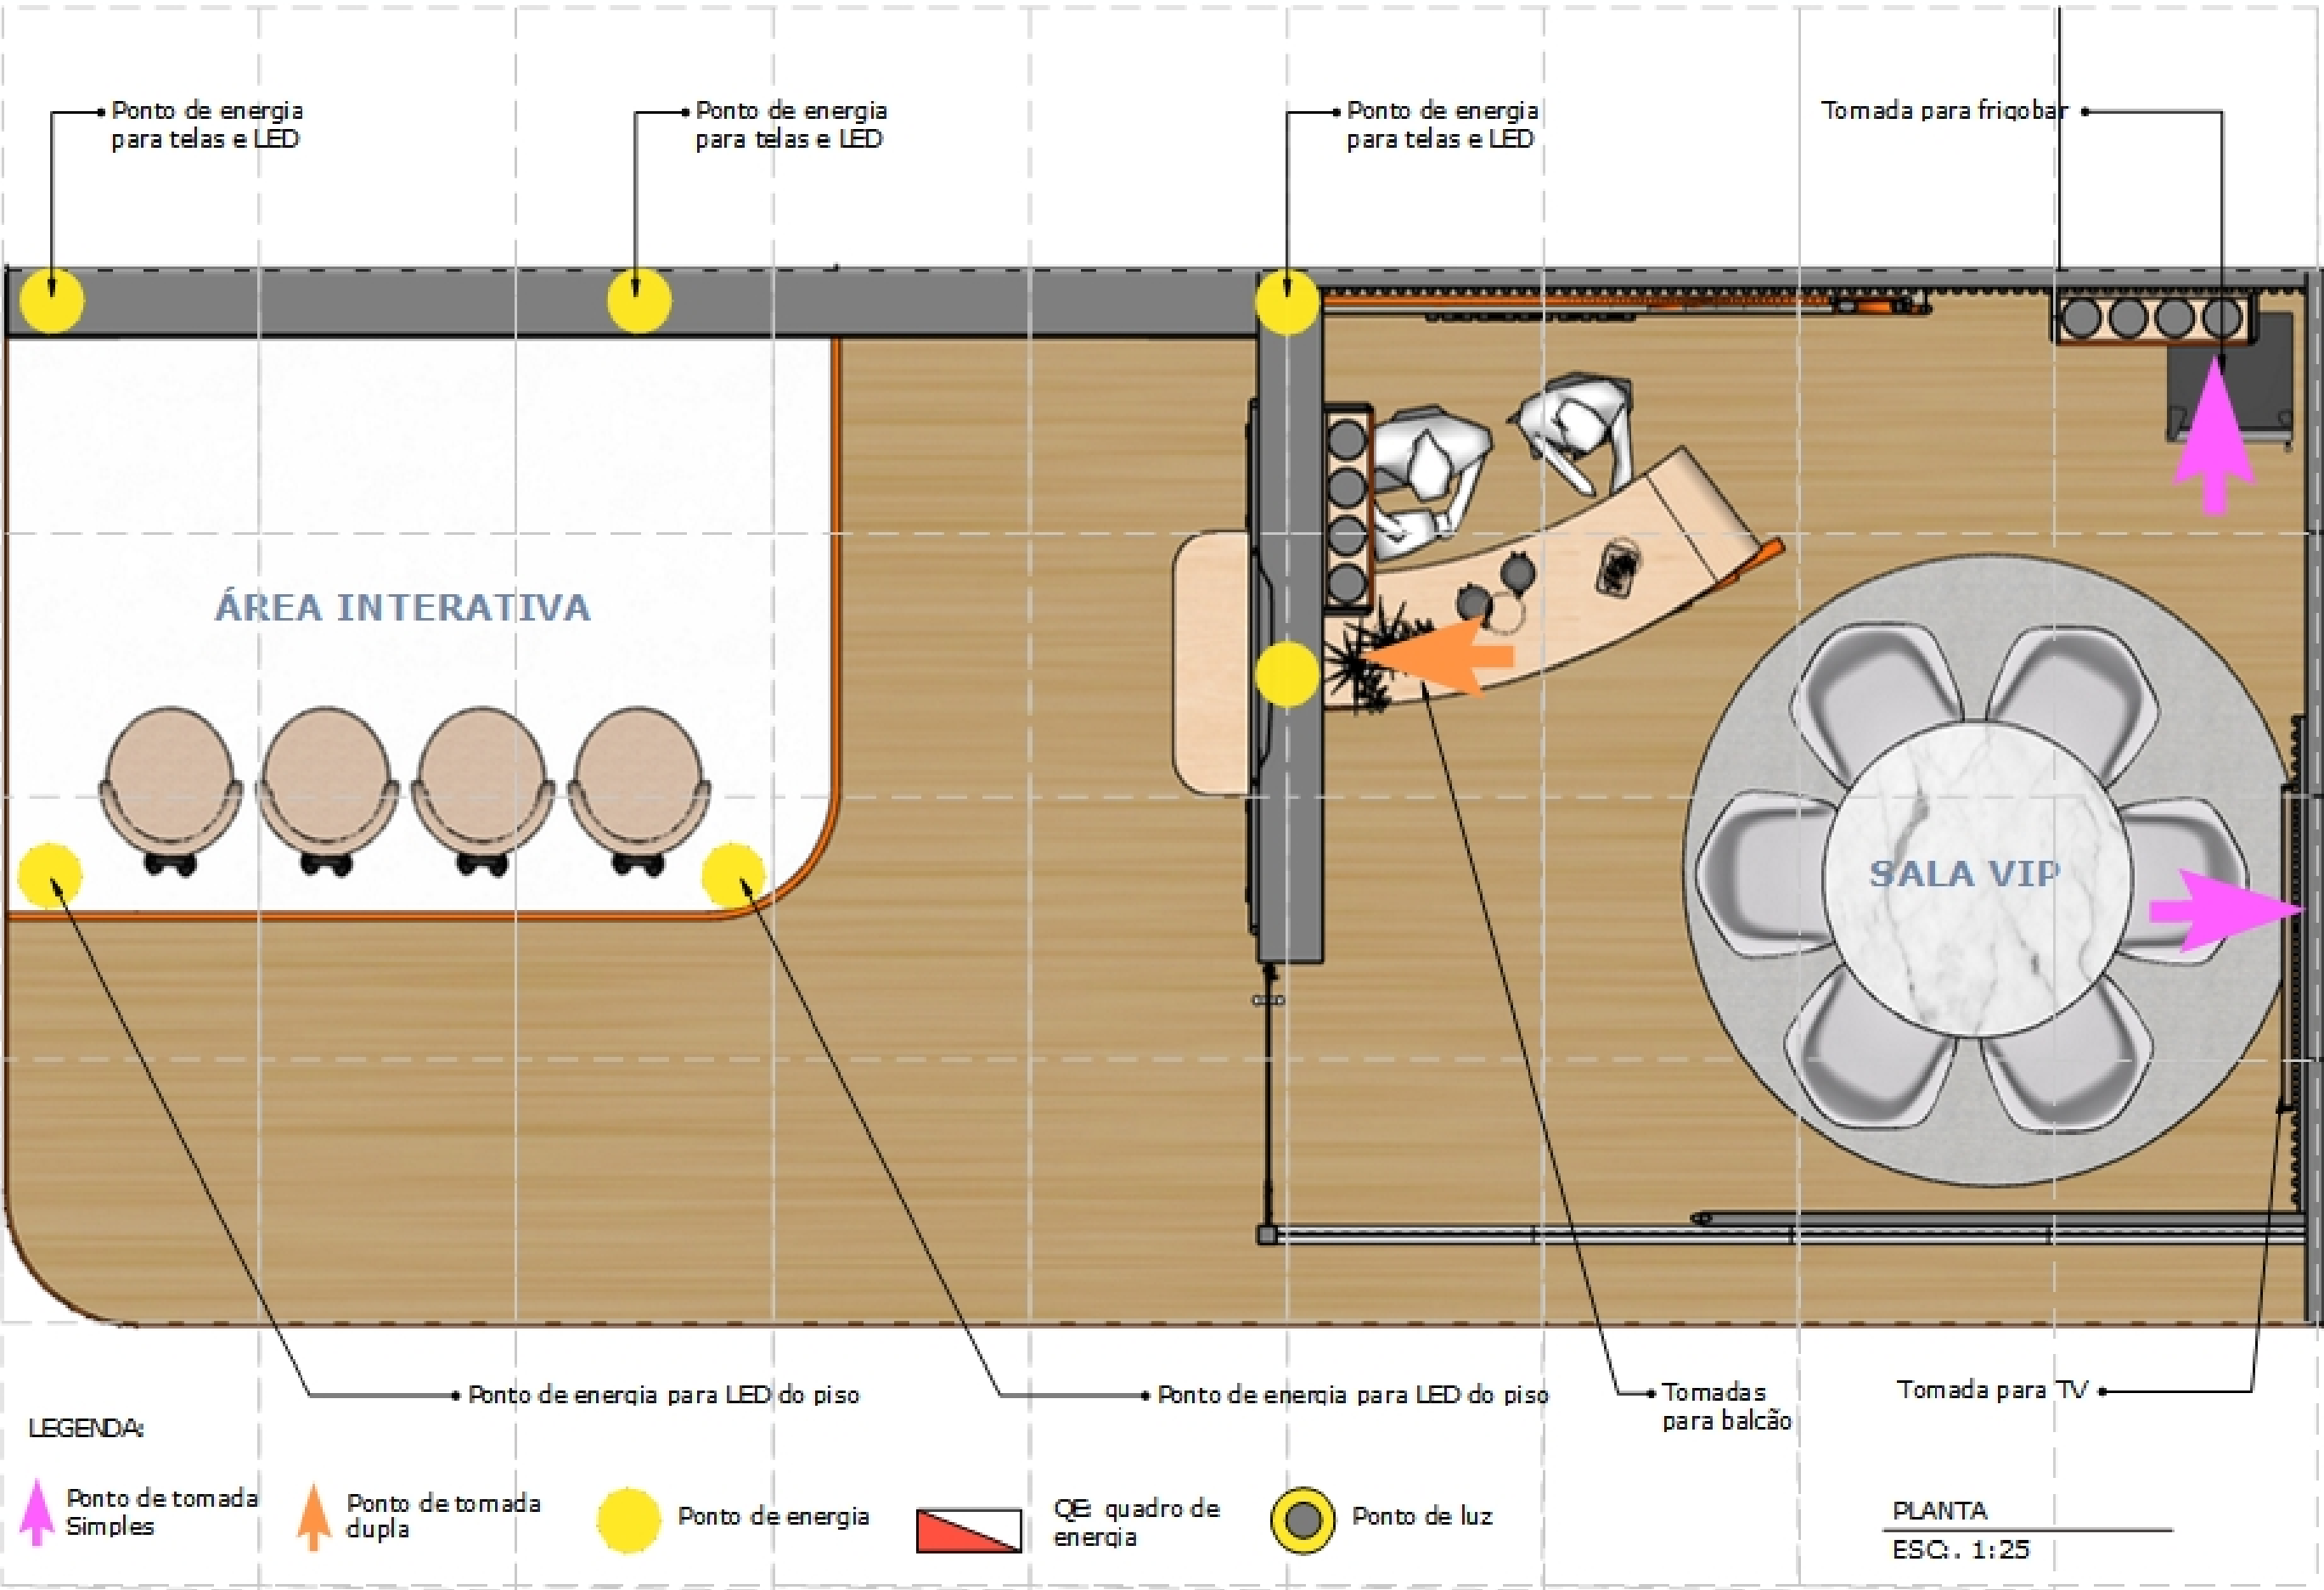

Todos os direitos reservados. Proibida a reprodução total ou parcial sem autorização prévia por escrito.

CORTE FRONTAL

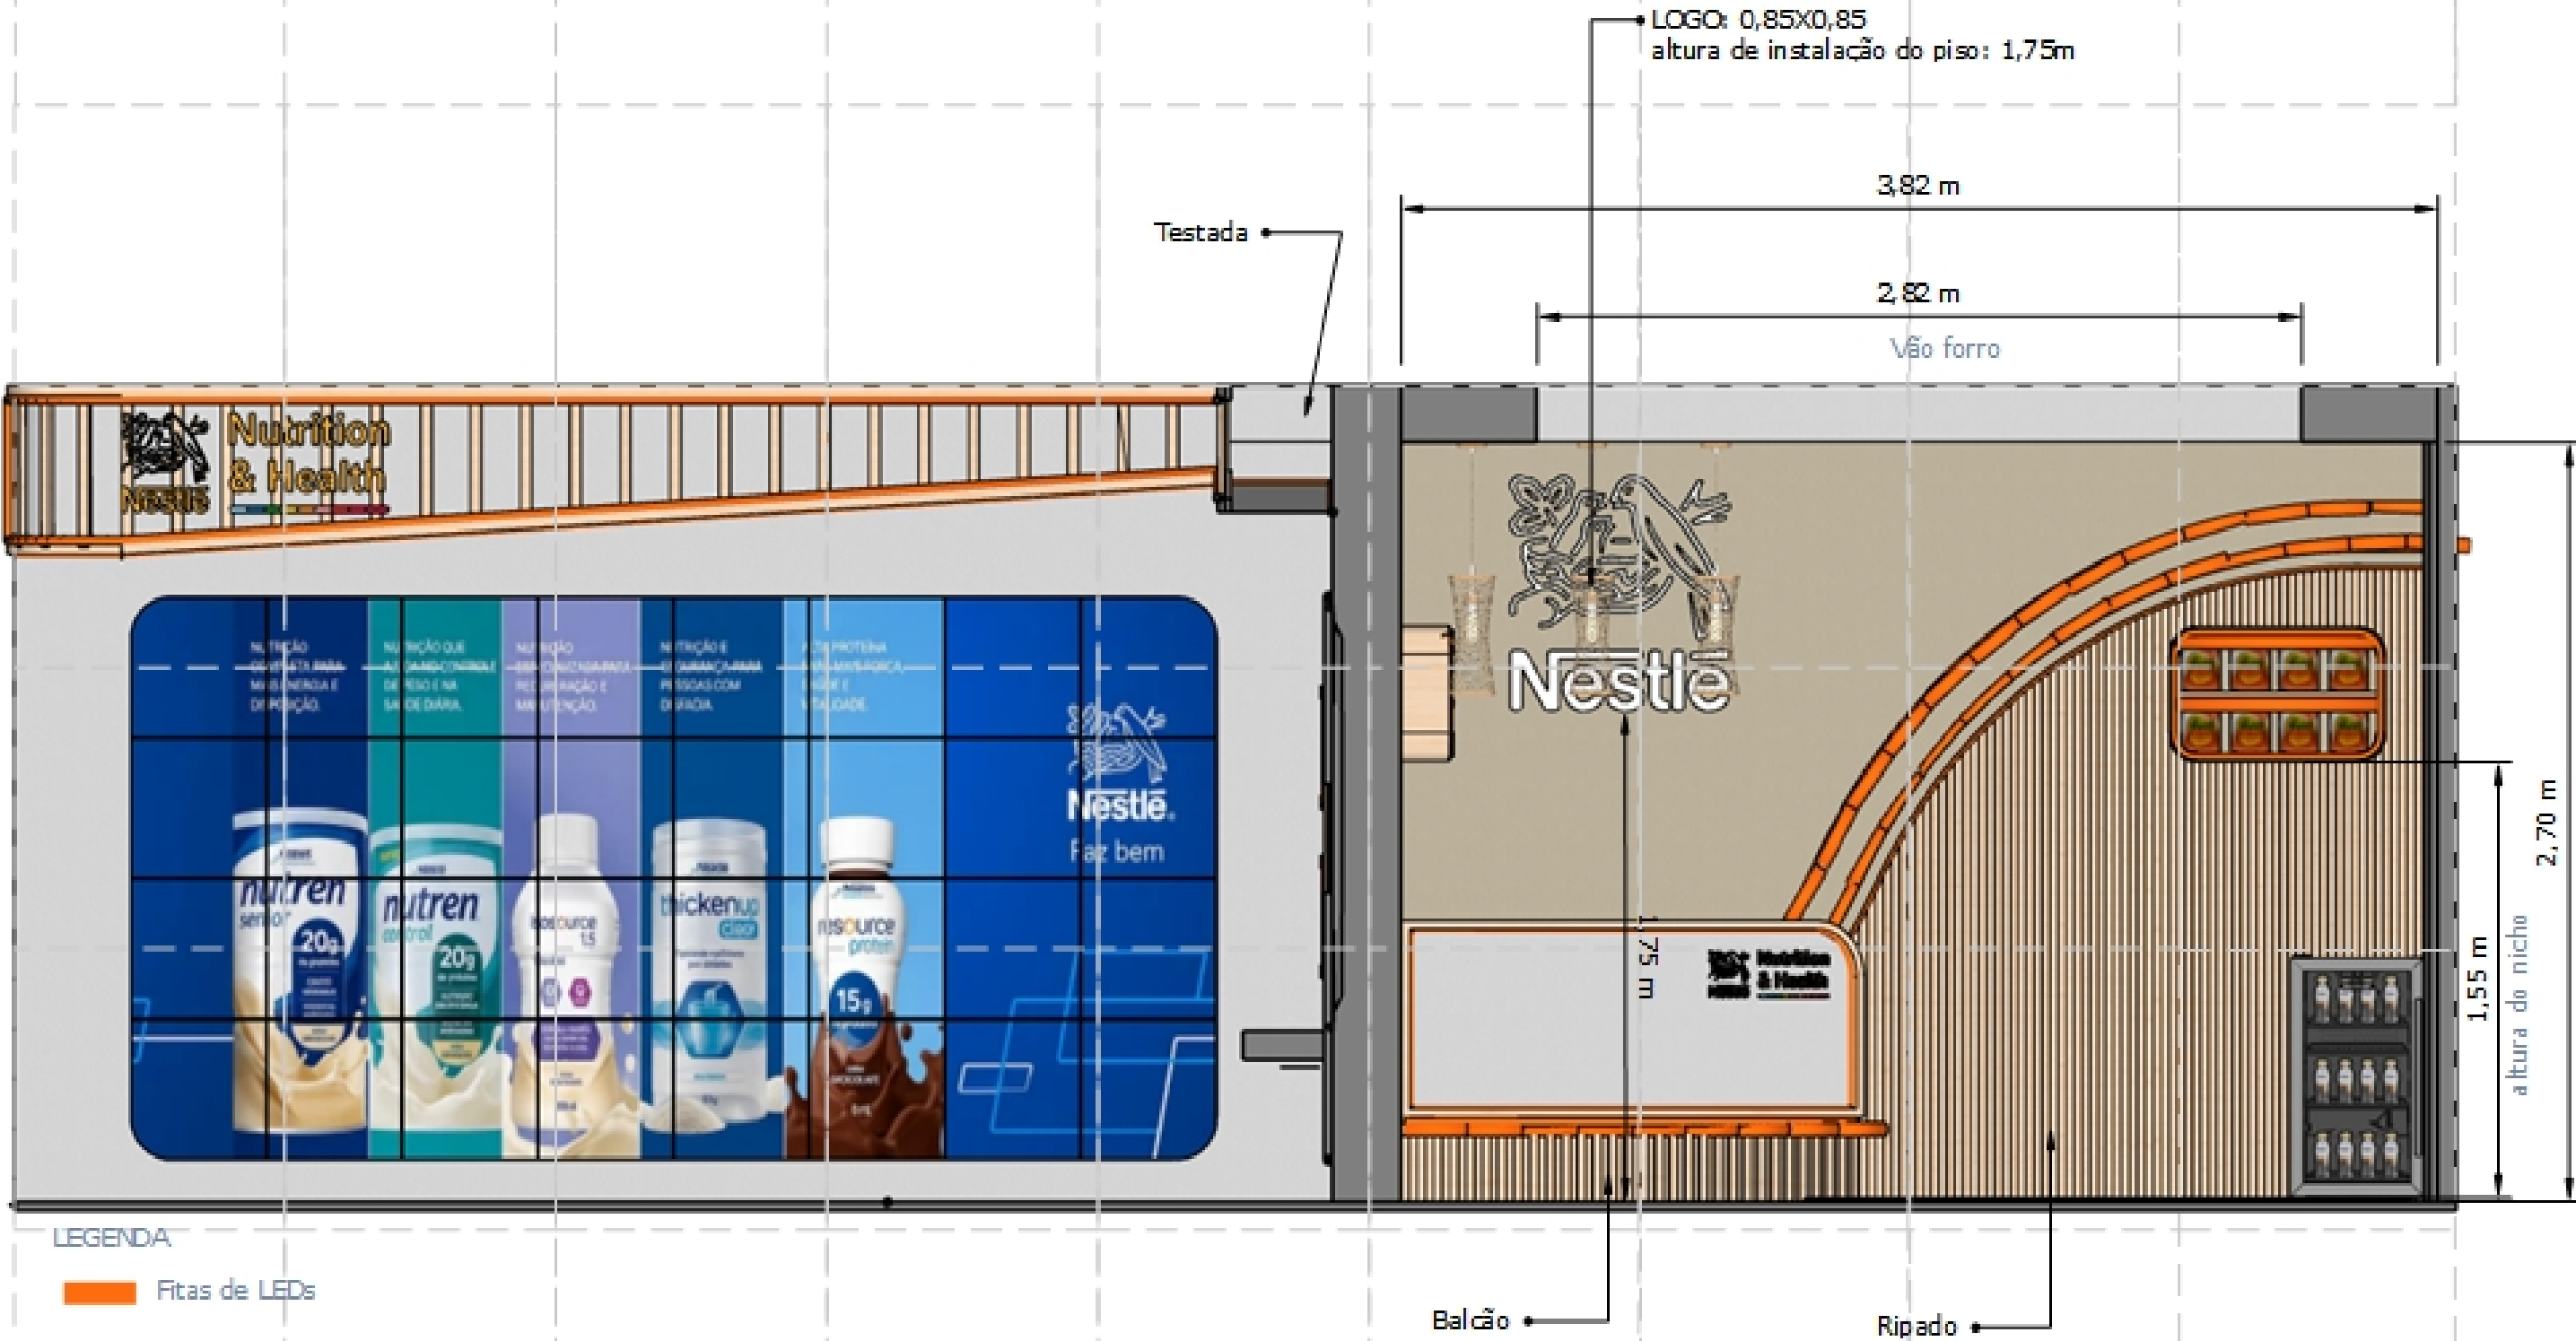

LEGENDA


Fitras de LEDs

CORTE FRONTAL


ESQ. 1:25

Malha de 1x1m


DETALHES DE PAREDE

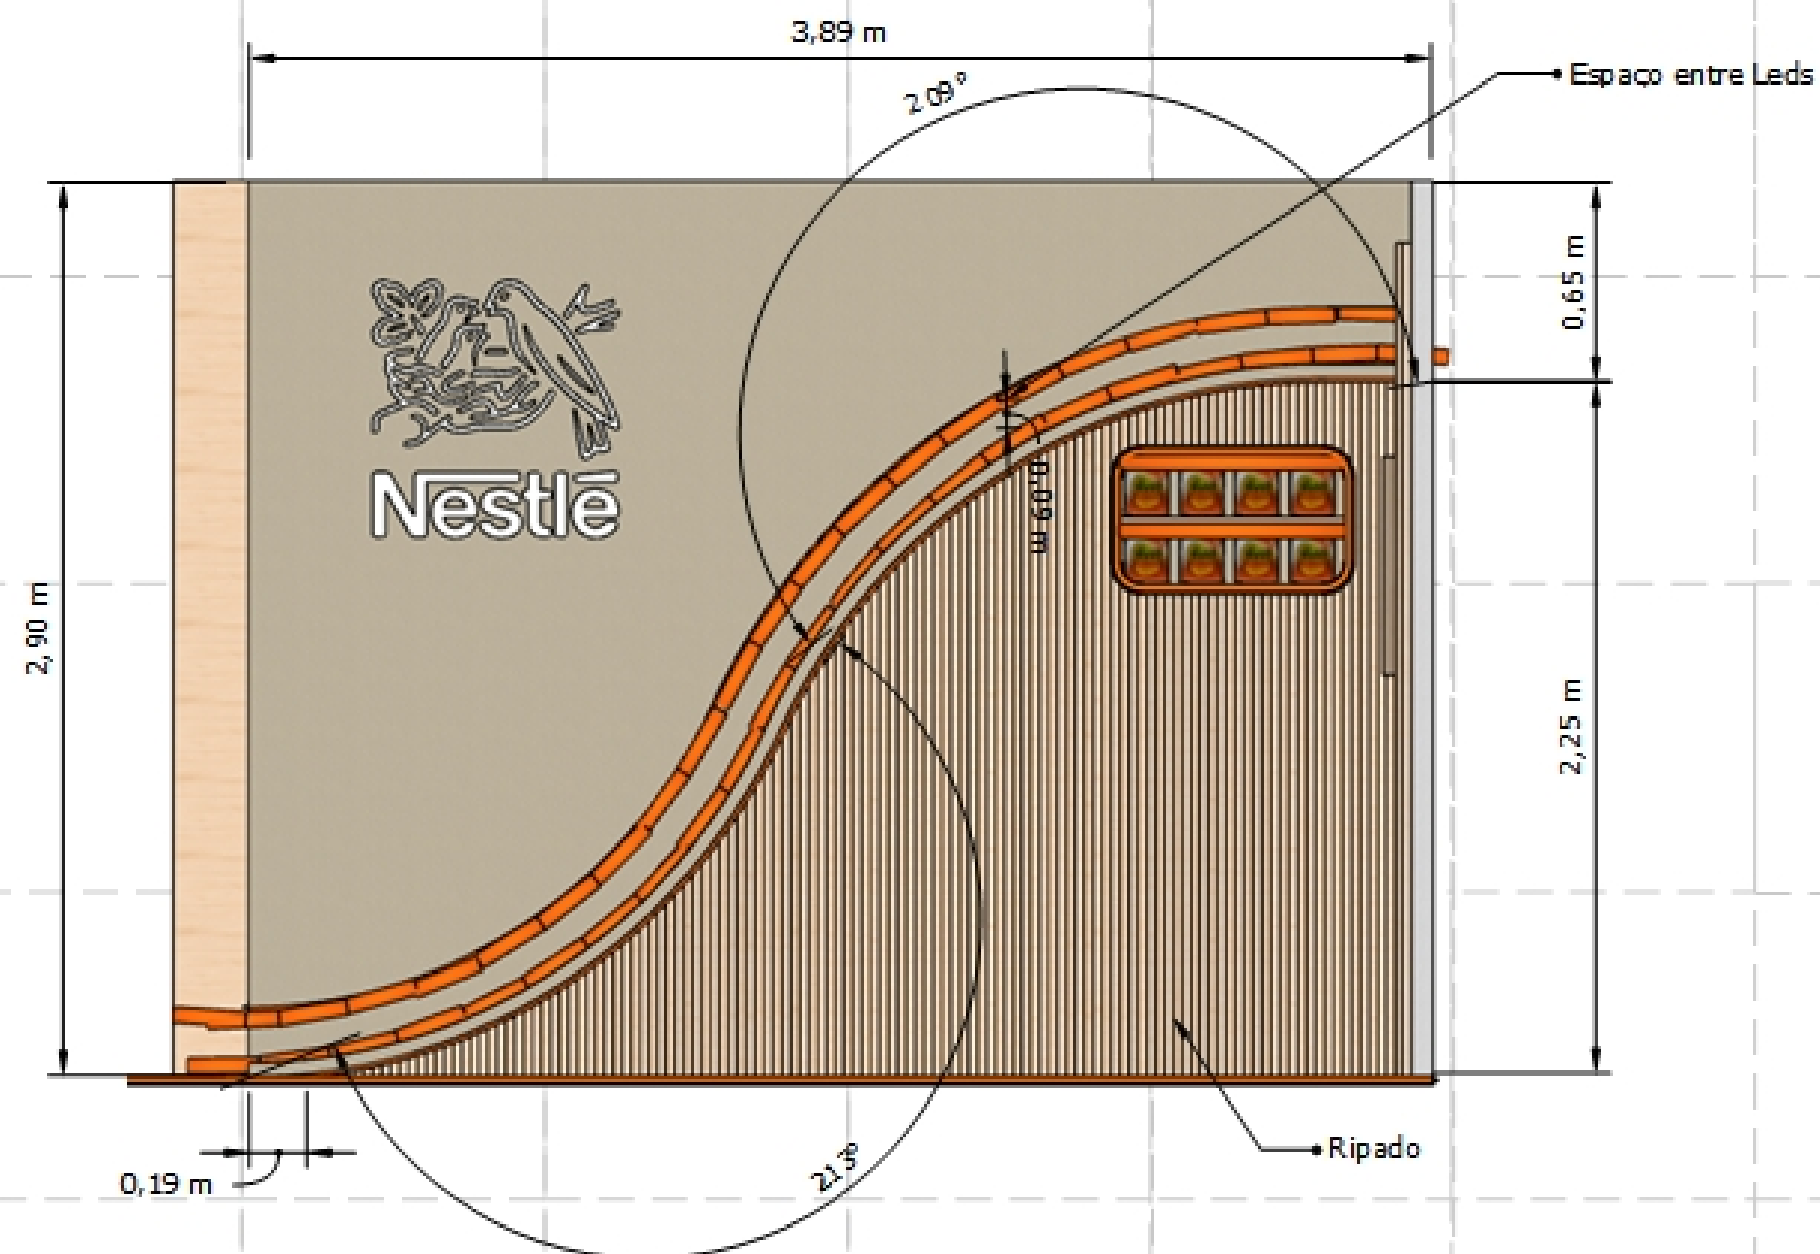

CORTE LATERAL ESQUERDA

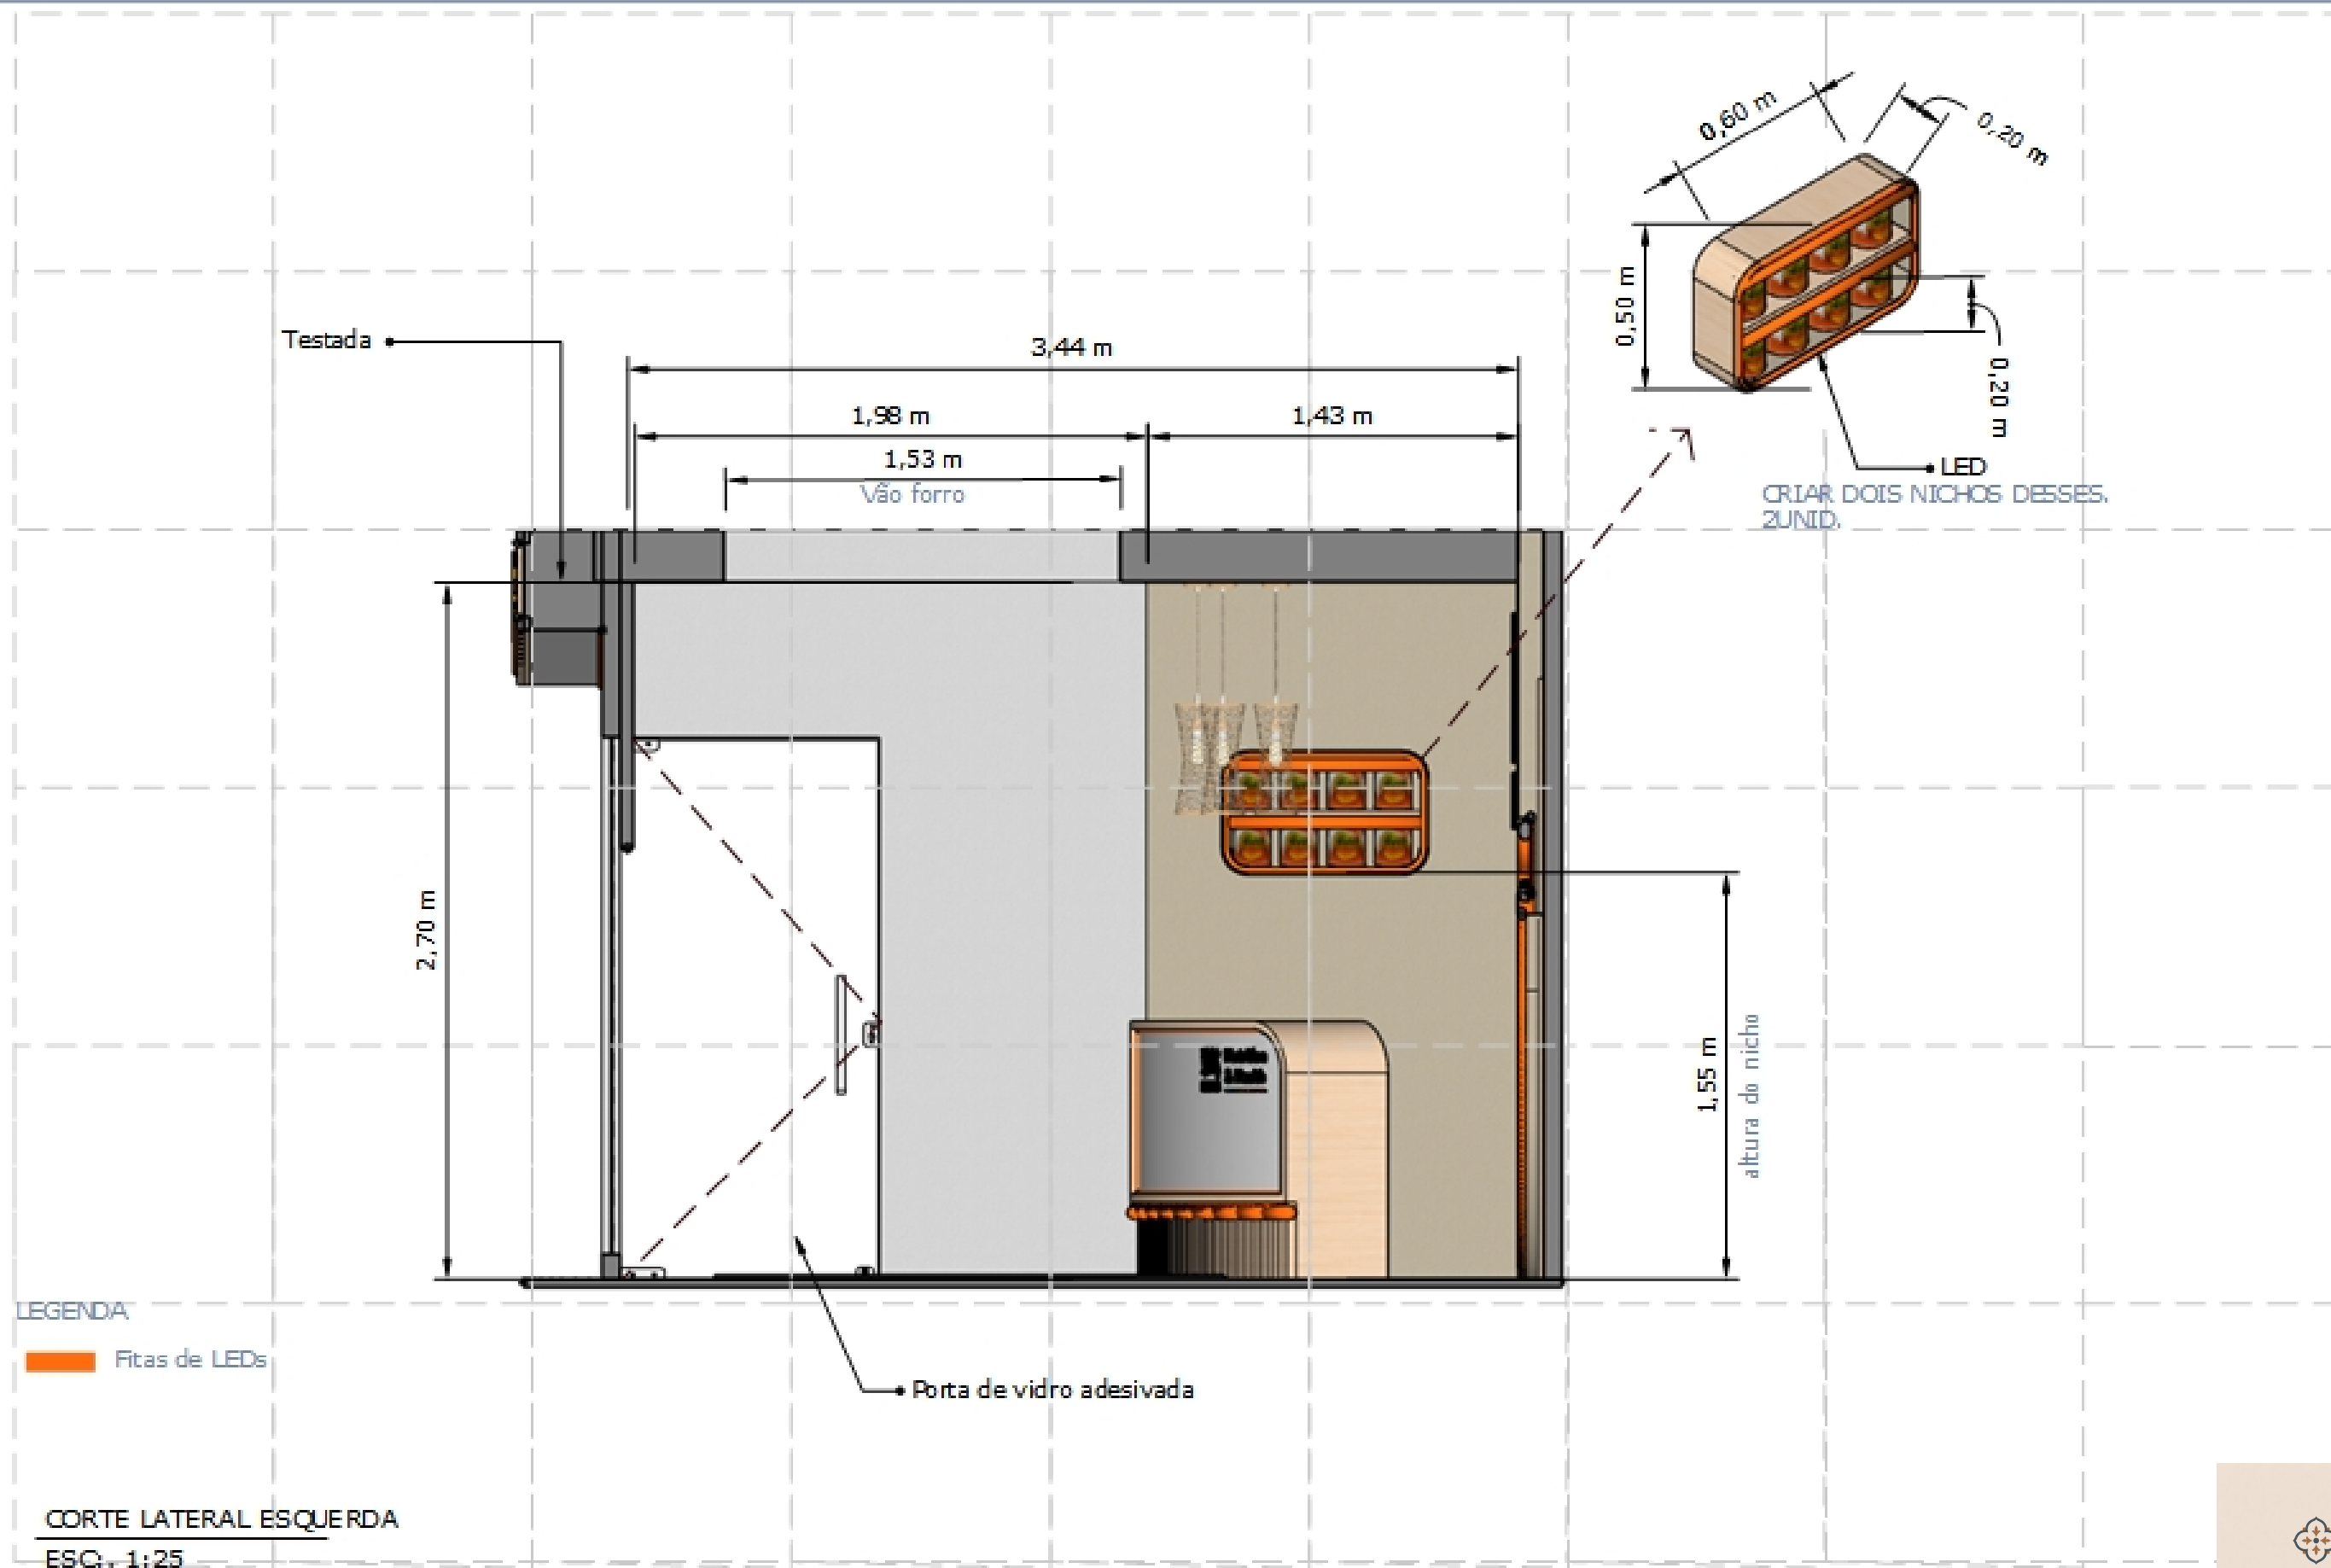

CORTE POSTERIOR

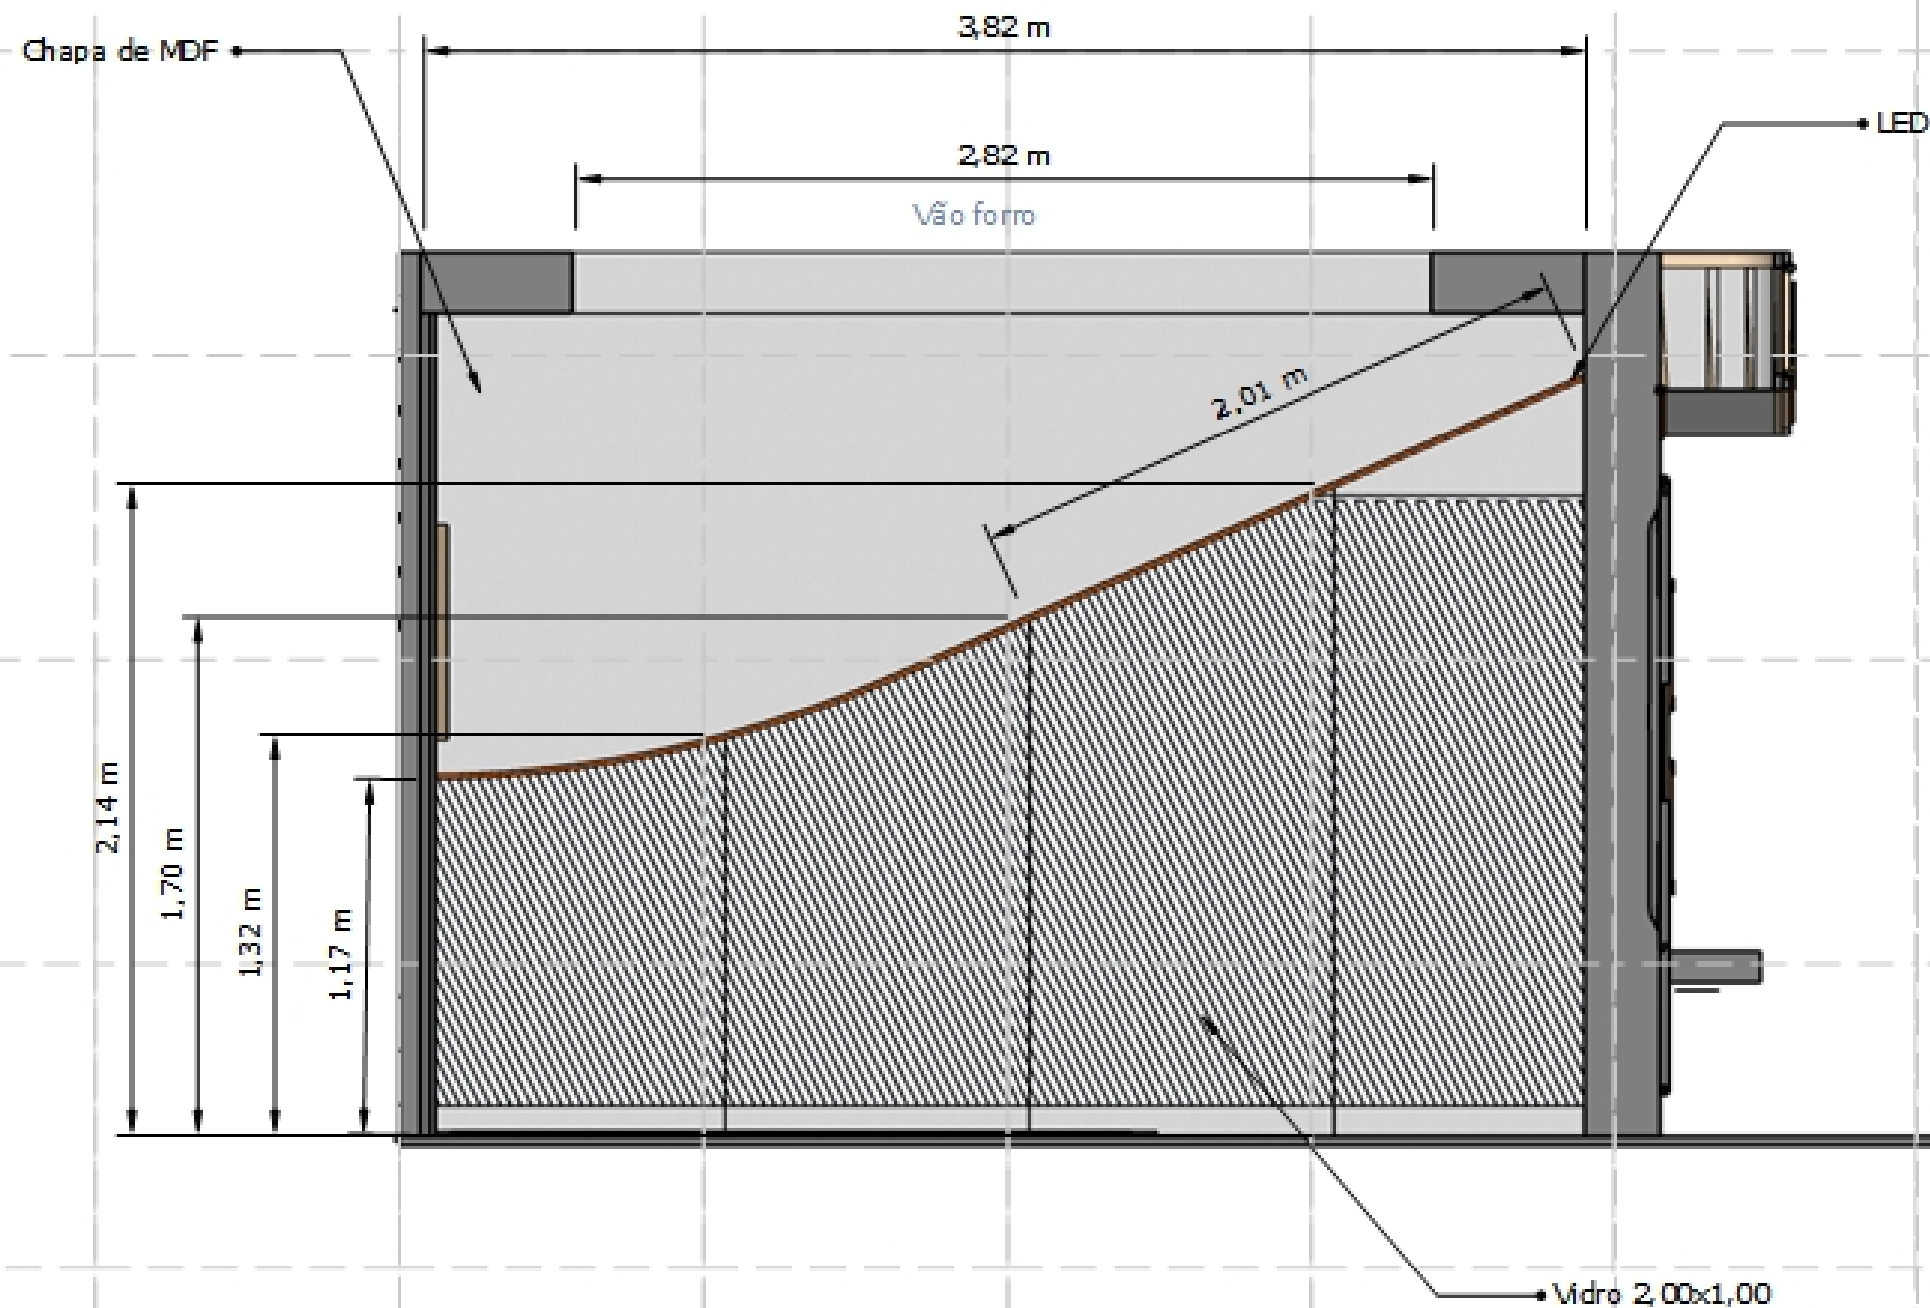

LEGENDA


 Fitas de LEDs

CORTE POSTERIOR


ESQ. 1:25

Malha de 1x1m

CORTE LATERAL DIREITA

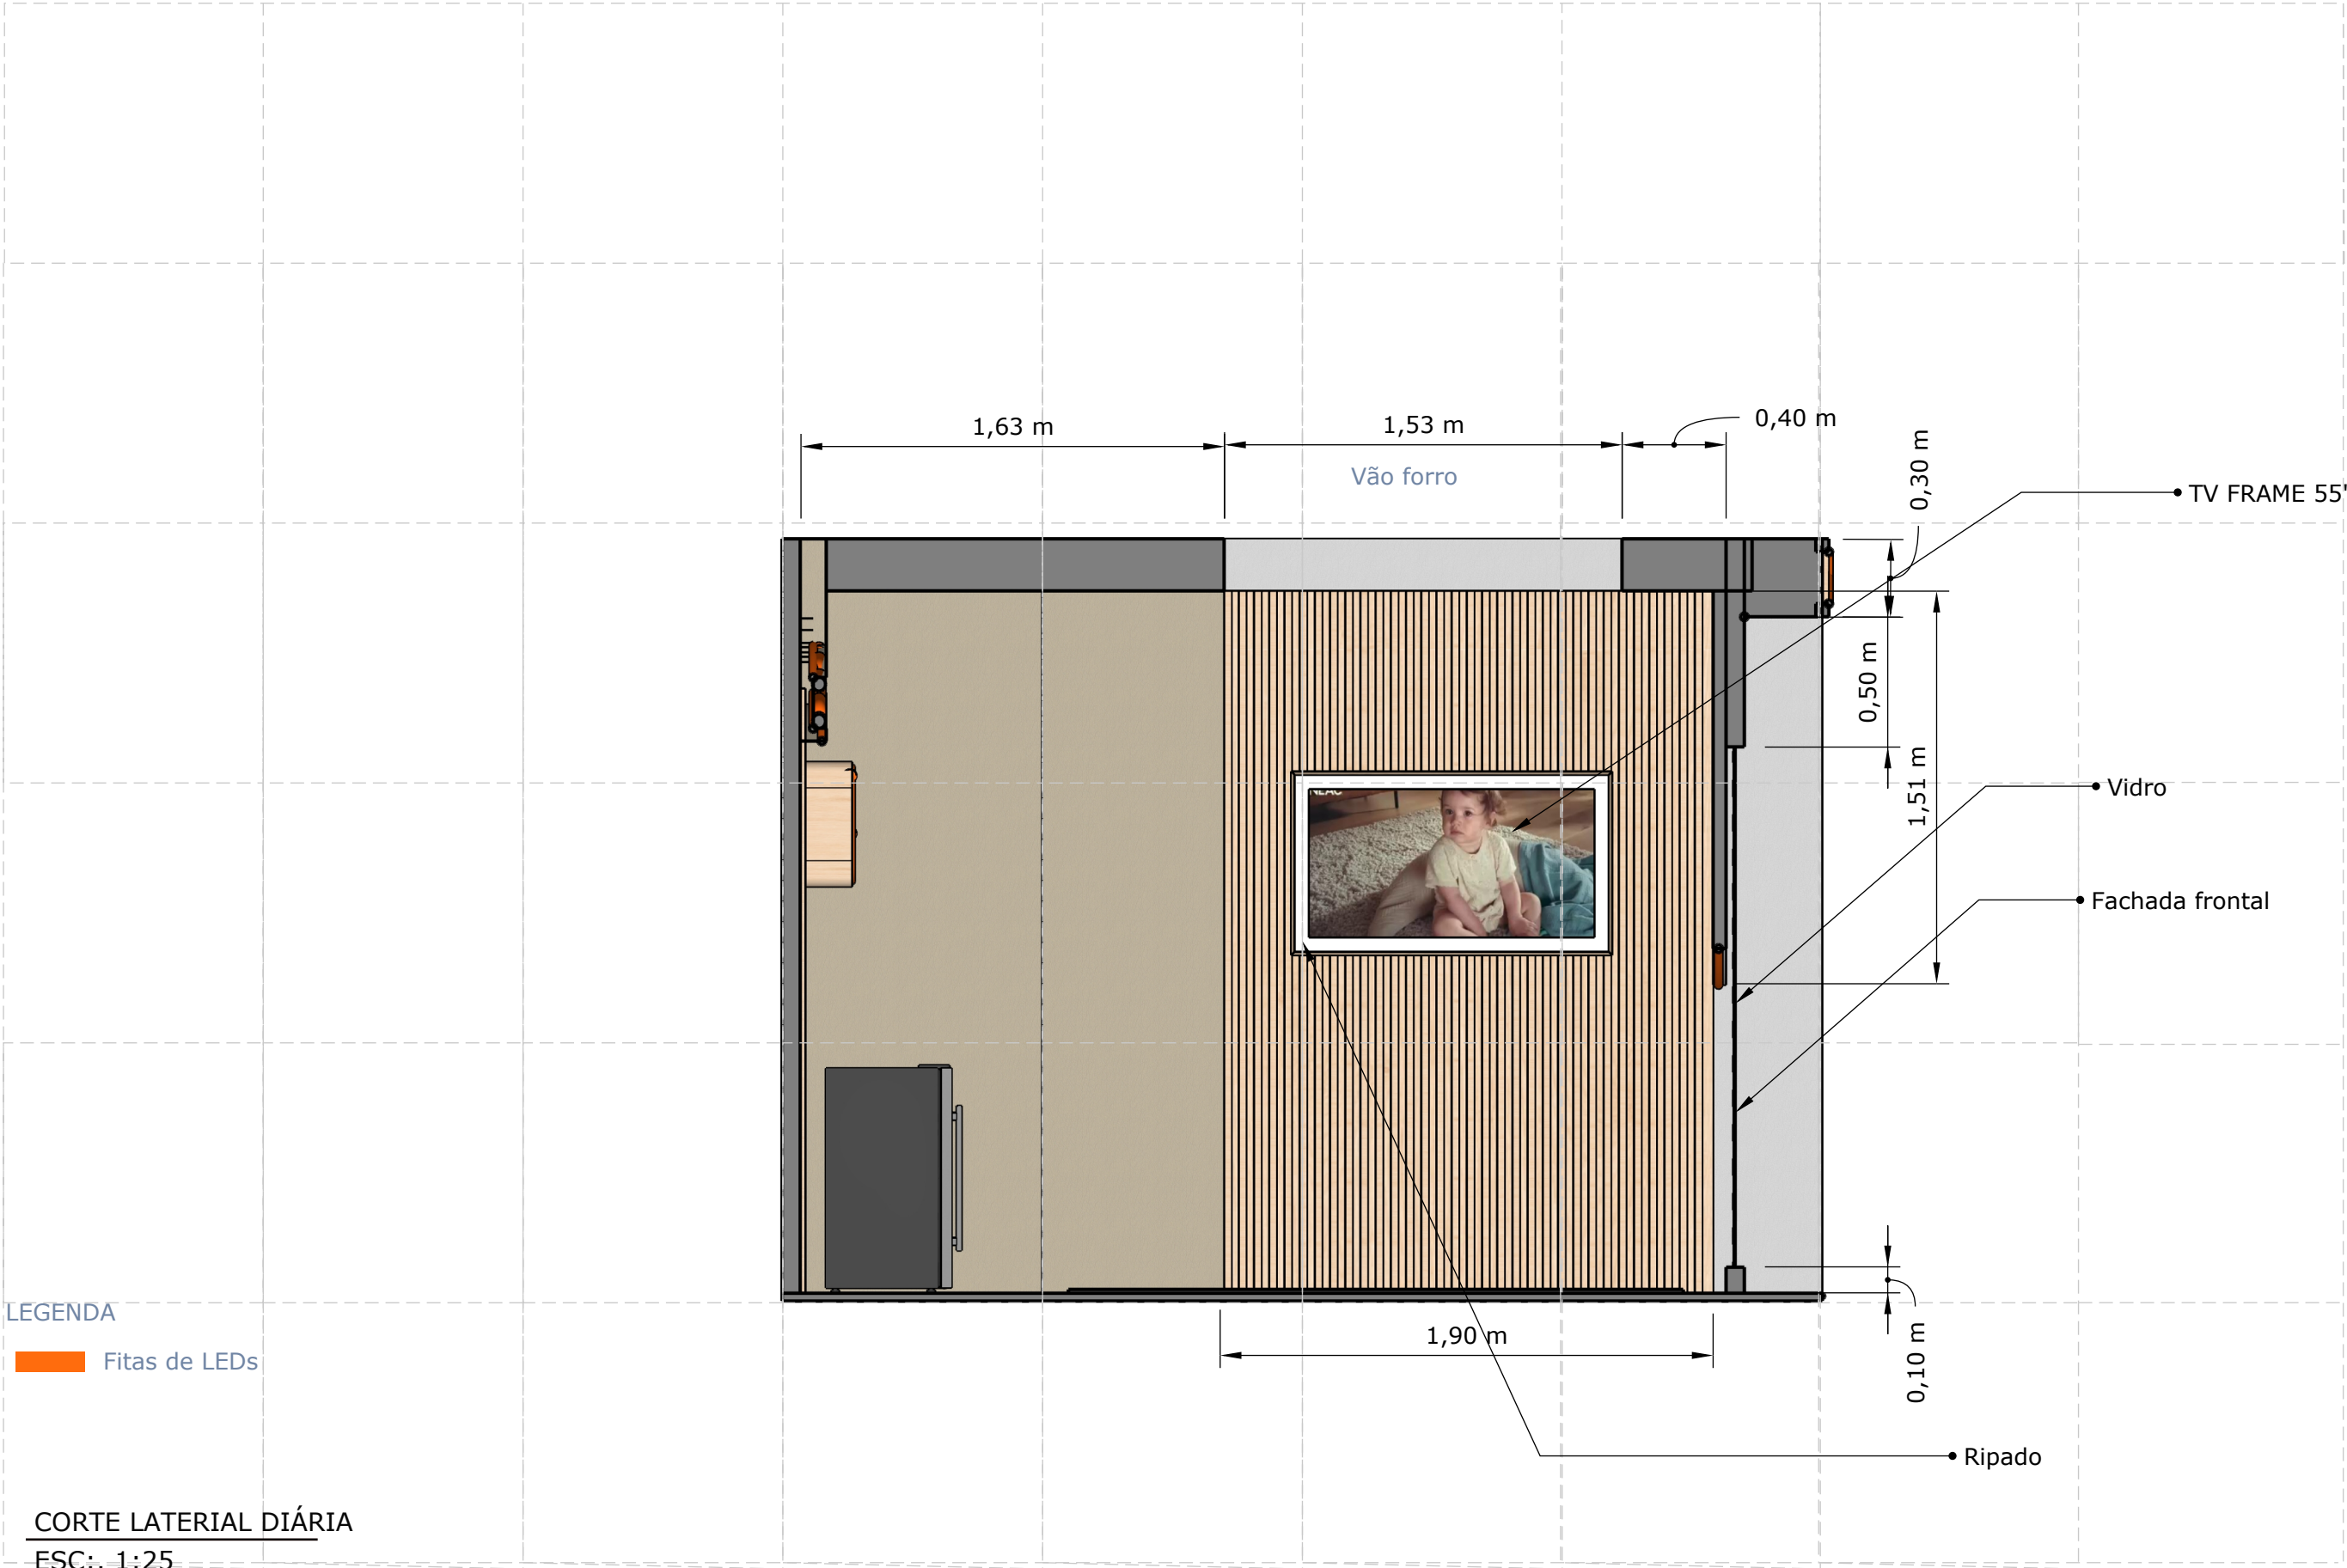

PERSPECTIVA PAREDES SALA VIP

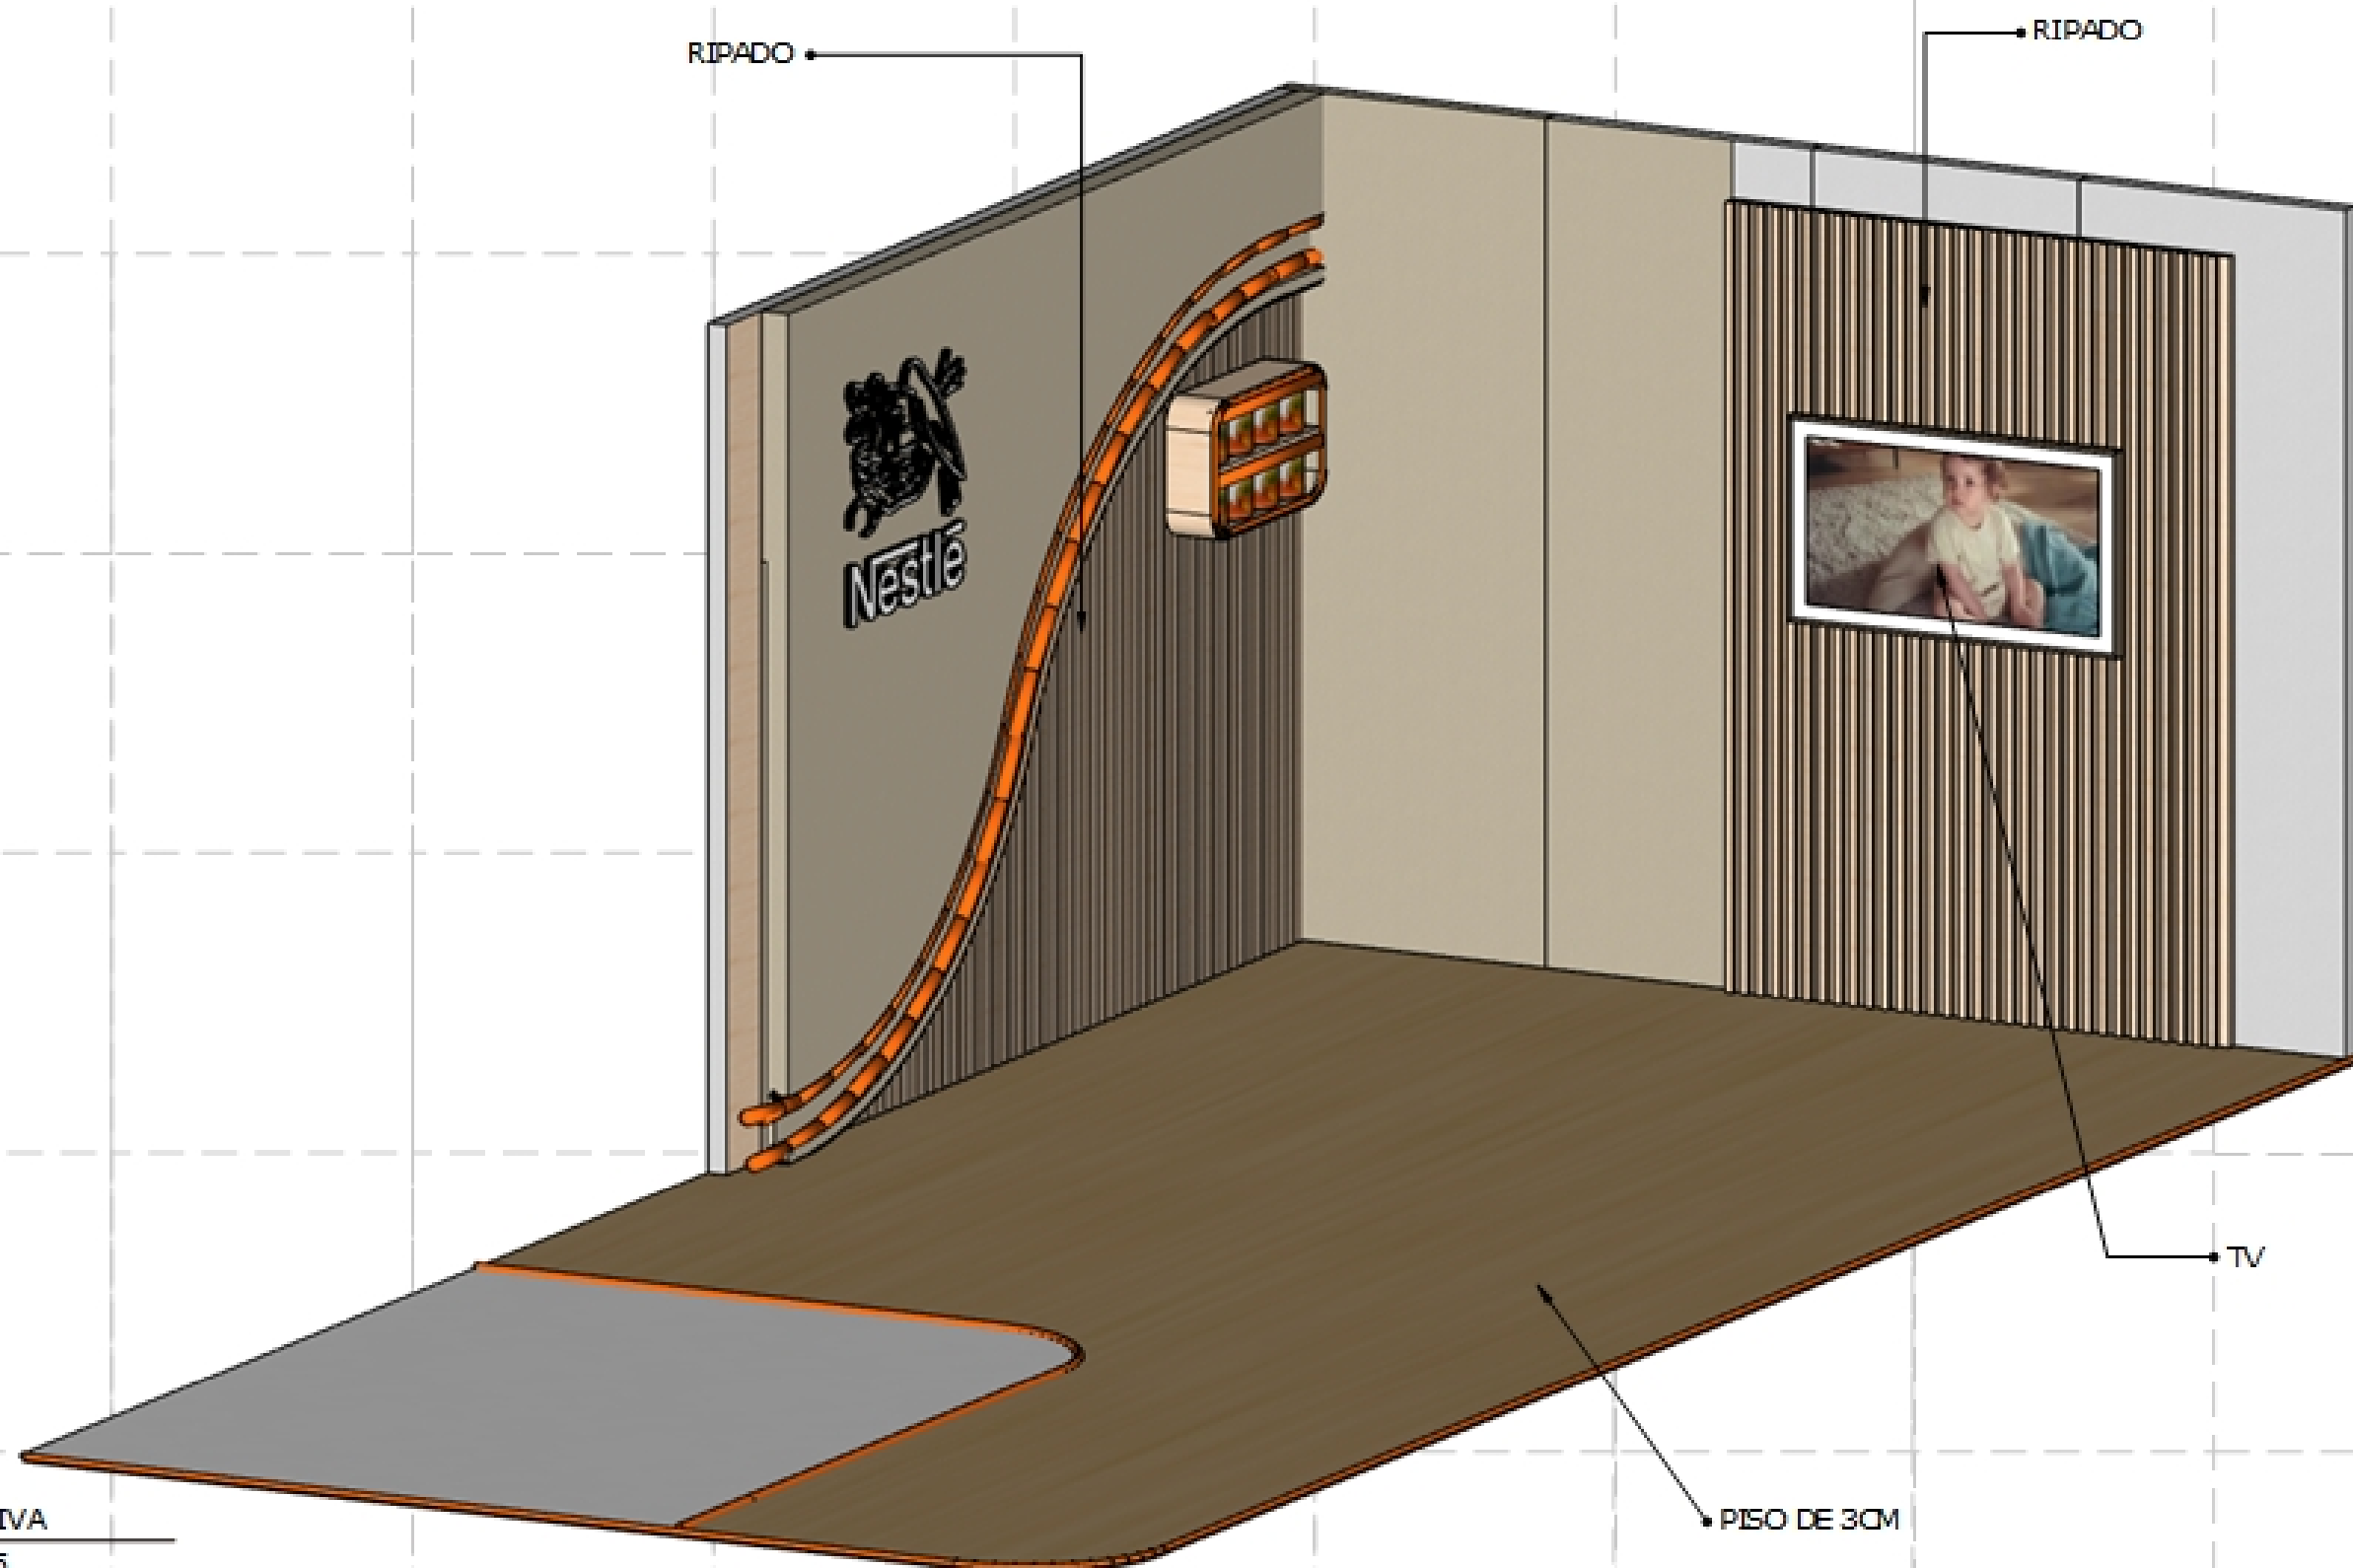

PERSPECTIVA
ESQ. 1:25

LEGENDA

 Fitas de LEDs

BALCÃO DE CAFÉ

